


S-01 DENAH TRIBUN

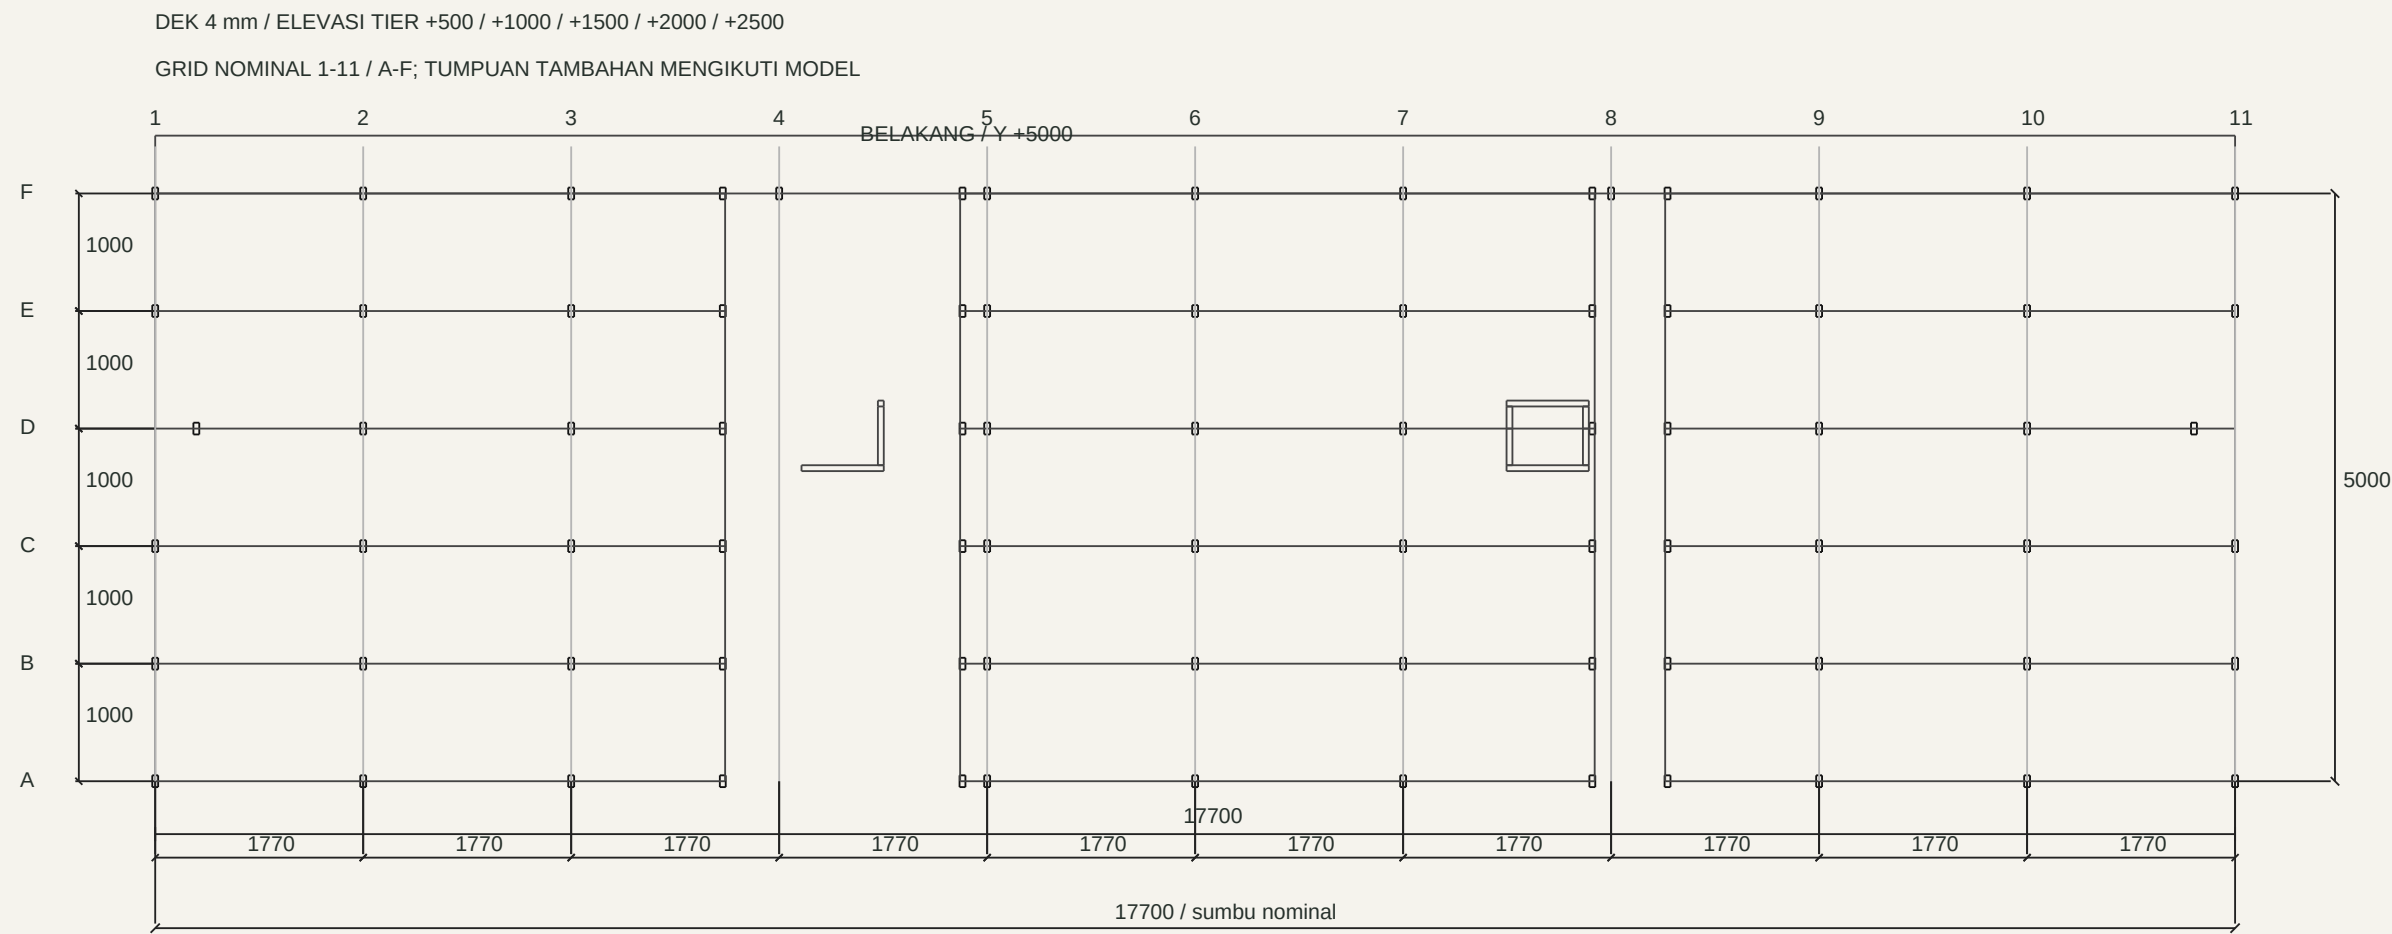


Dek bordes 4 mm. Proyeksi batas luar model; bukaan di sekitar beton harus disurvei.

Area BOQ 82,345 m2 dari parameter Revit; bukan luas proyeksi persegi gambar ini.

LOD 200: bentuk, ukuran dan posisi perkiraan. Detail sambungan mengikuti status masing-masing.

SATUAN: mm | PDF: FIT / NTS | DIMENSI NOMINAL KOORDINASI | DETAIL TERSEDIA DIPERTAHANKAN

S-02 RENCANA TUMPUAN

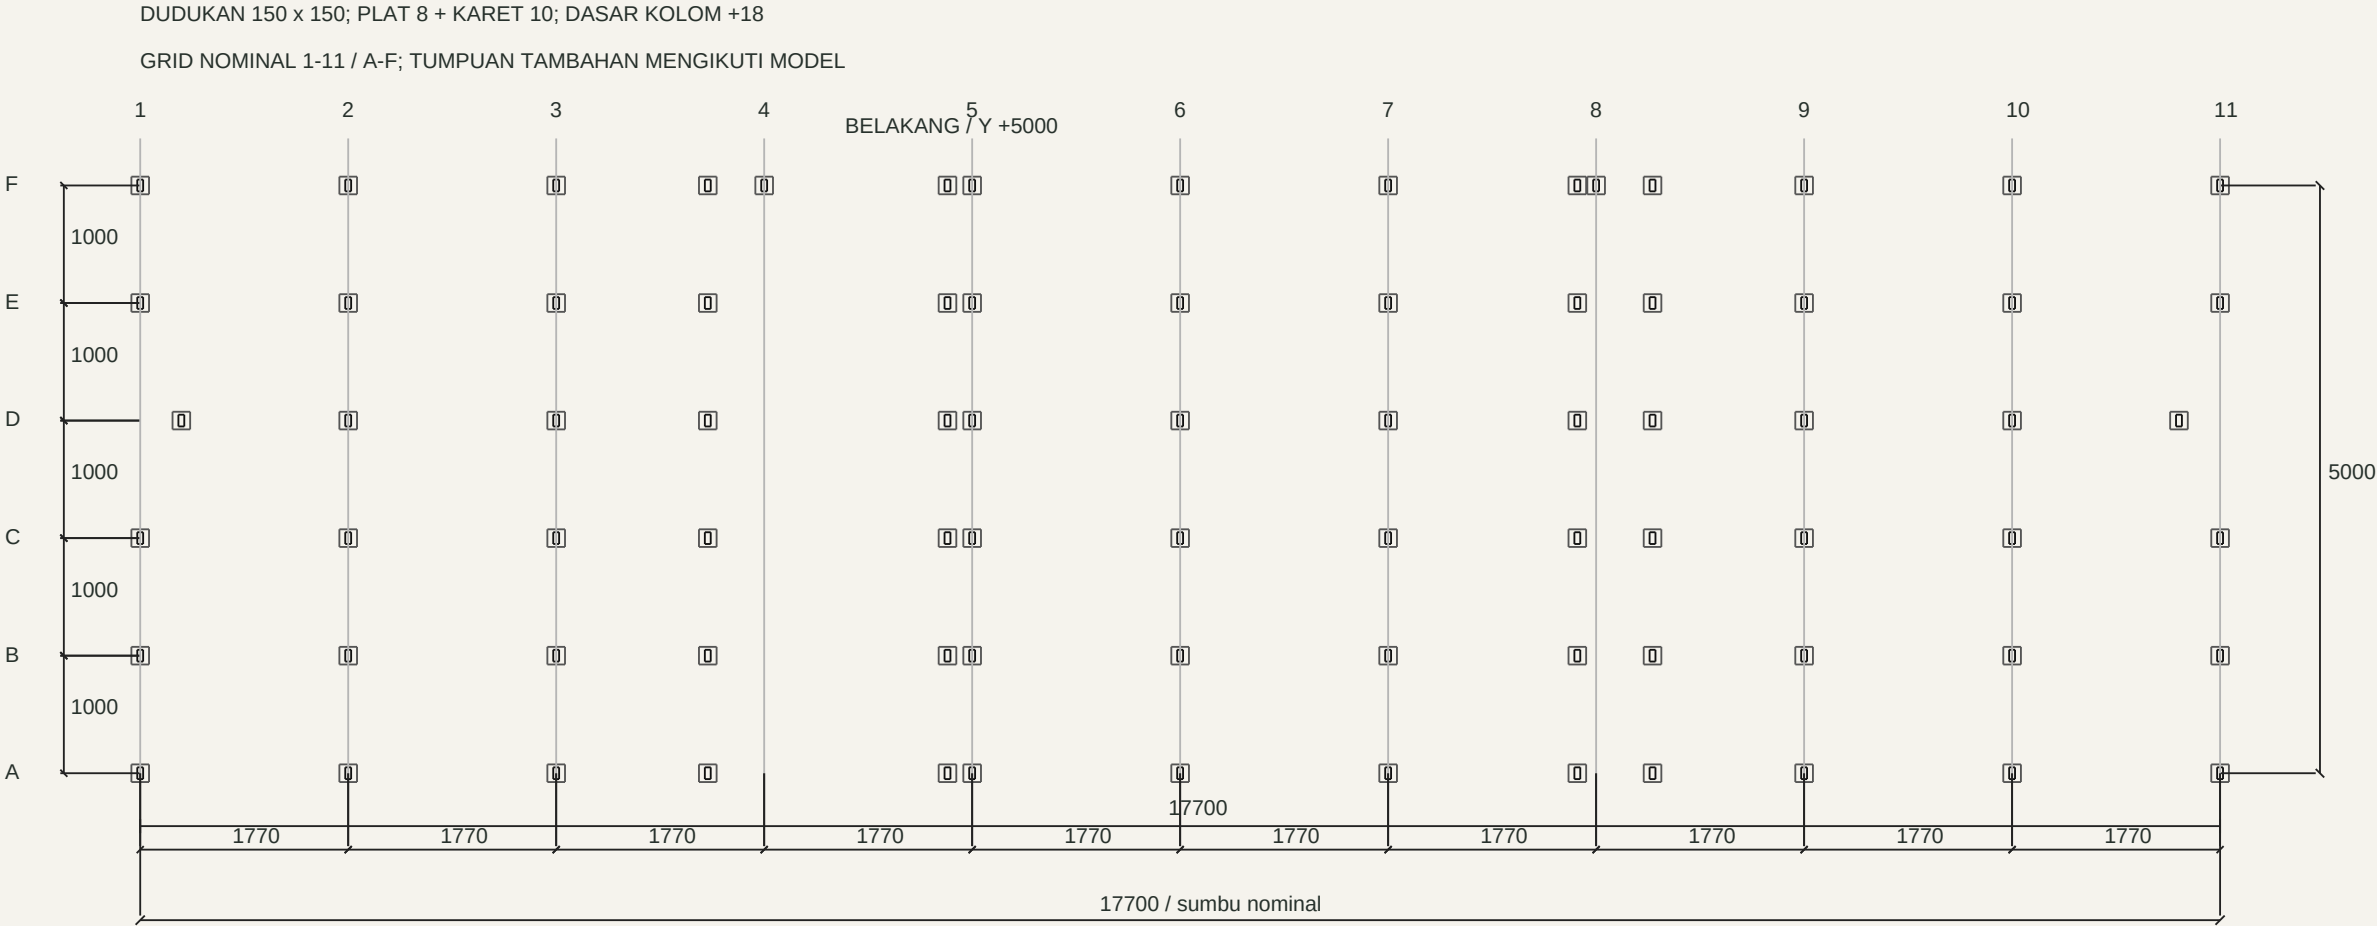


80 kolom, 80 base plate 150x150x8, 80 karet 150x150x10.

Dasar kolom +18 mm. Dudukan lepas tidak otomatis menjadi sendi yang menahan geser/angkat.

LOD 200: bentuk, ukuran dan posisi perkiraan. Detail sambungan mengikuti status masing-masing.

SATUAN: mm | PDF: FIT / NTS | DIMENSI NOMINAL KOORDINASI | DETAIL TERSEDIA DIPERTAHANKAN

S-03 RENCANA RANGKA & X

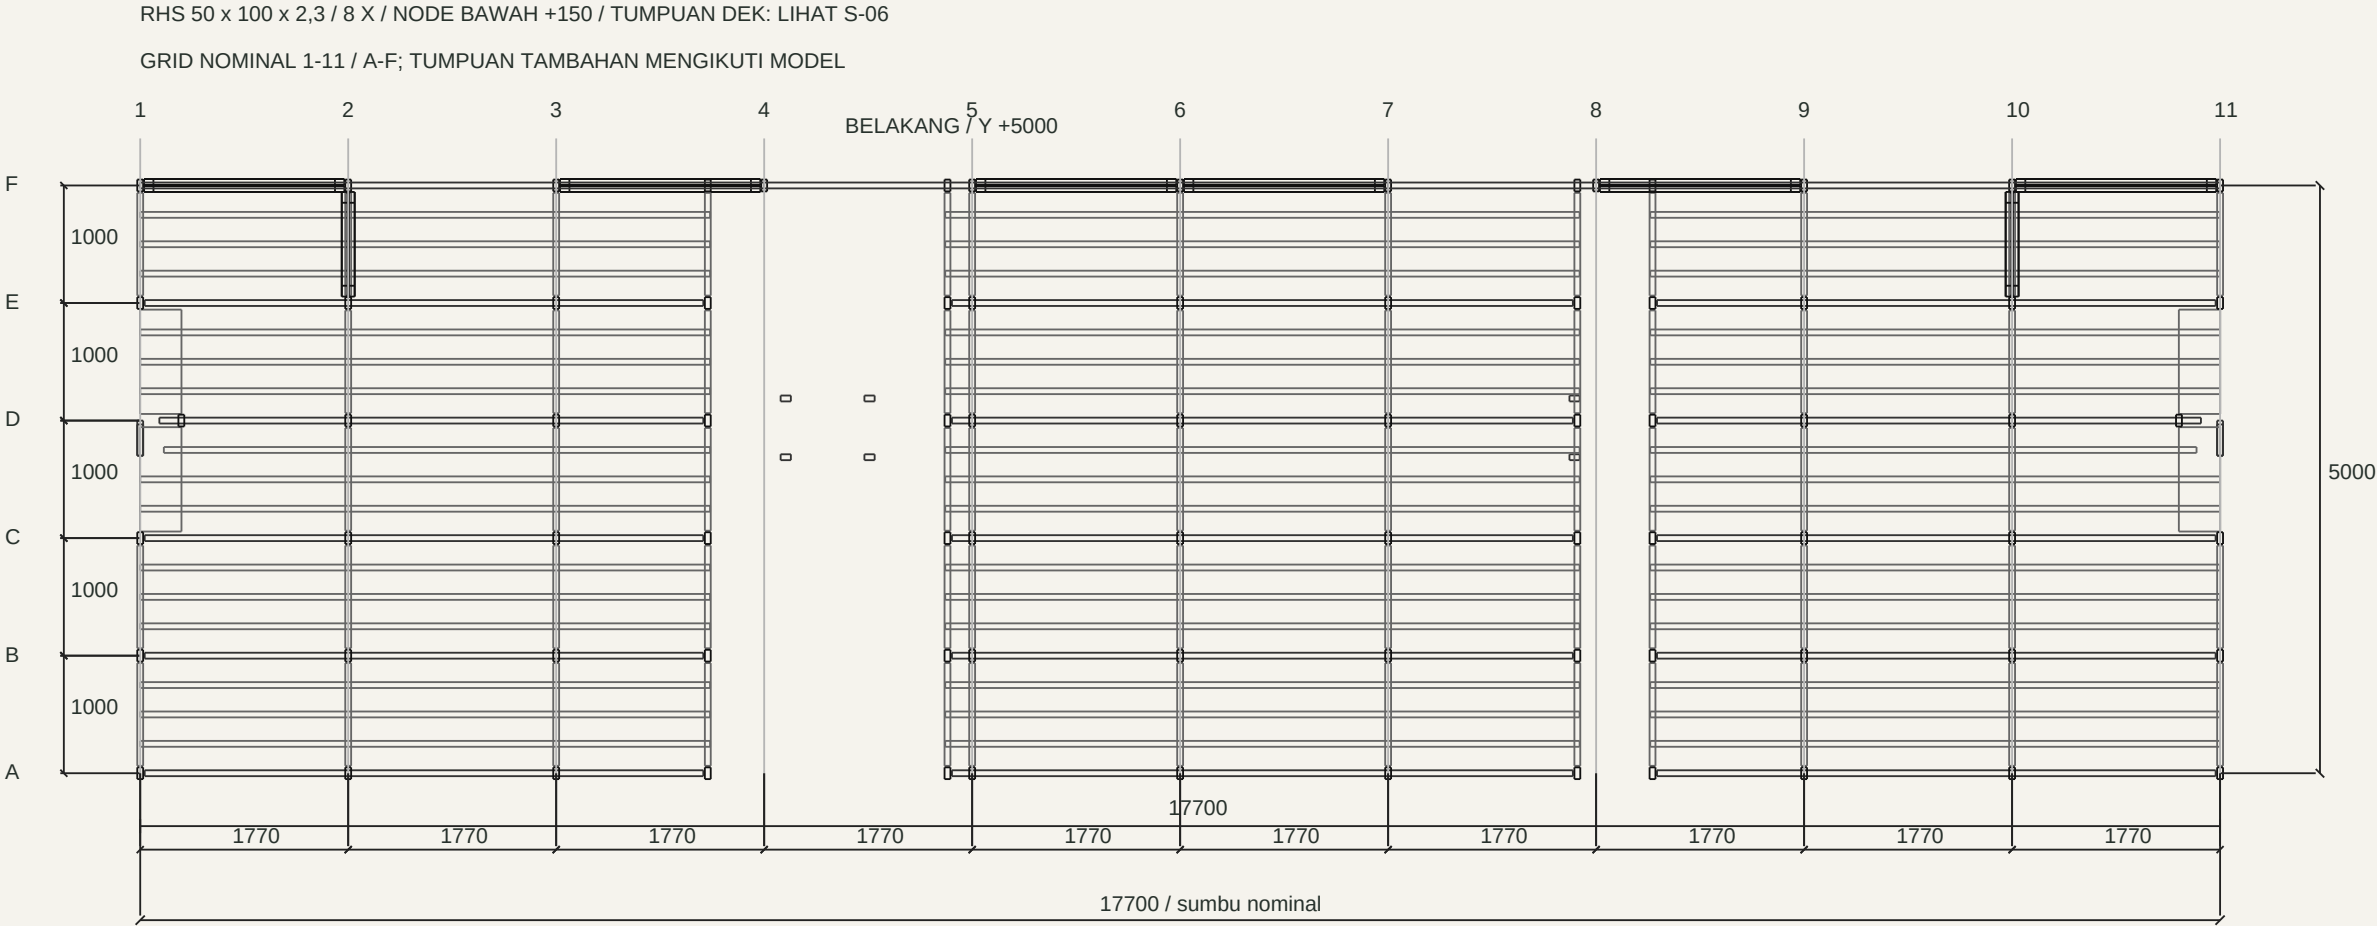

161 RHS 50x100x2,3 termasuk 16 diagonal / 8 X. Node bawah +150 mm.


45 joist longitudinal dan 65 balok silang mengikuti revisi model; celah sambungan belum final.

LOD 200: bentuk, ukuran dan posisi perkiraan. Detail sambungan mengikuti status masing-masing.

SATUAN: mm | PDF: FIT / NTS | DIMENSI NOMINAL KOORDINASI | DETAIL TERSEDIA DIPERTAHANKAN

S-04 TAMPAK DEPAN

RHS 50 x 100 x 2,3 / DEK 4 / TINGGI NOMINAL DARI LT4 +0

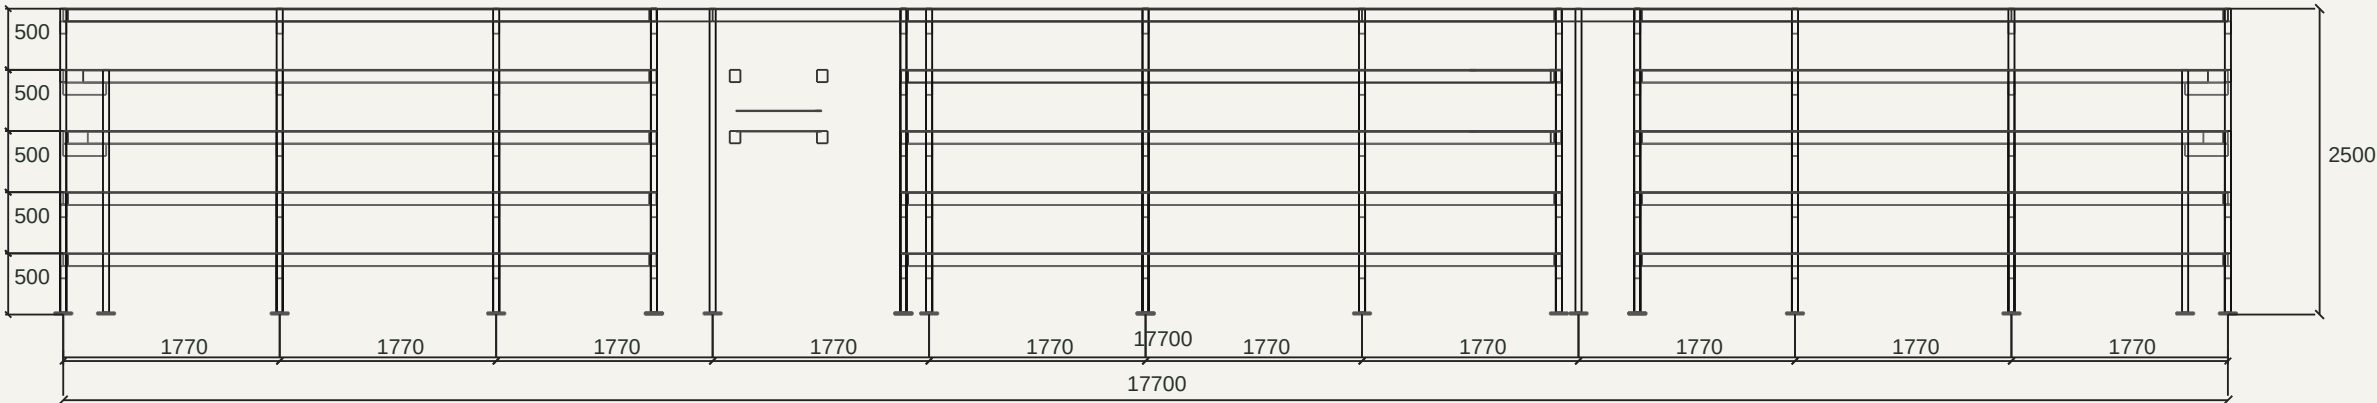


Proyeksi rangka dari lapangan. Semua tingkat terlihat transparan; garis belakang tidak dihapus.

Finishing, railing dan tangga perlu dicocokkan dengan model arsitektur.

LOD 200: bentuk, ukuran dan posisi perkiraan. Detail sambungan mengikuti status masing-masing.

SATUAN: mm | PDF: FIT / NTS | DIMENSI NOMINAL KOORDINASI | DETAIL TERSEDIA DIPERTAHANKAN

S-05 TAMPAK SAMPING

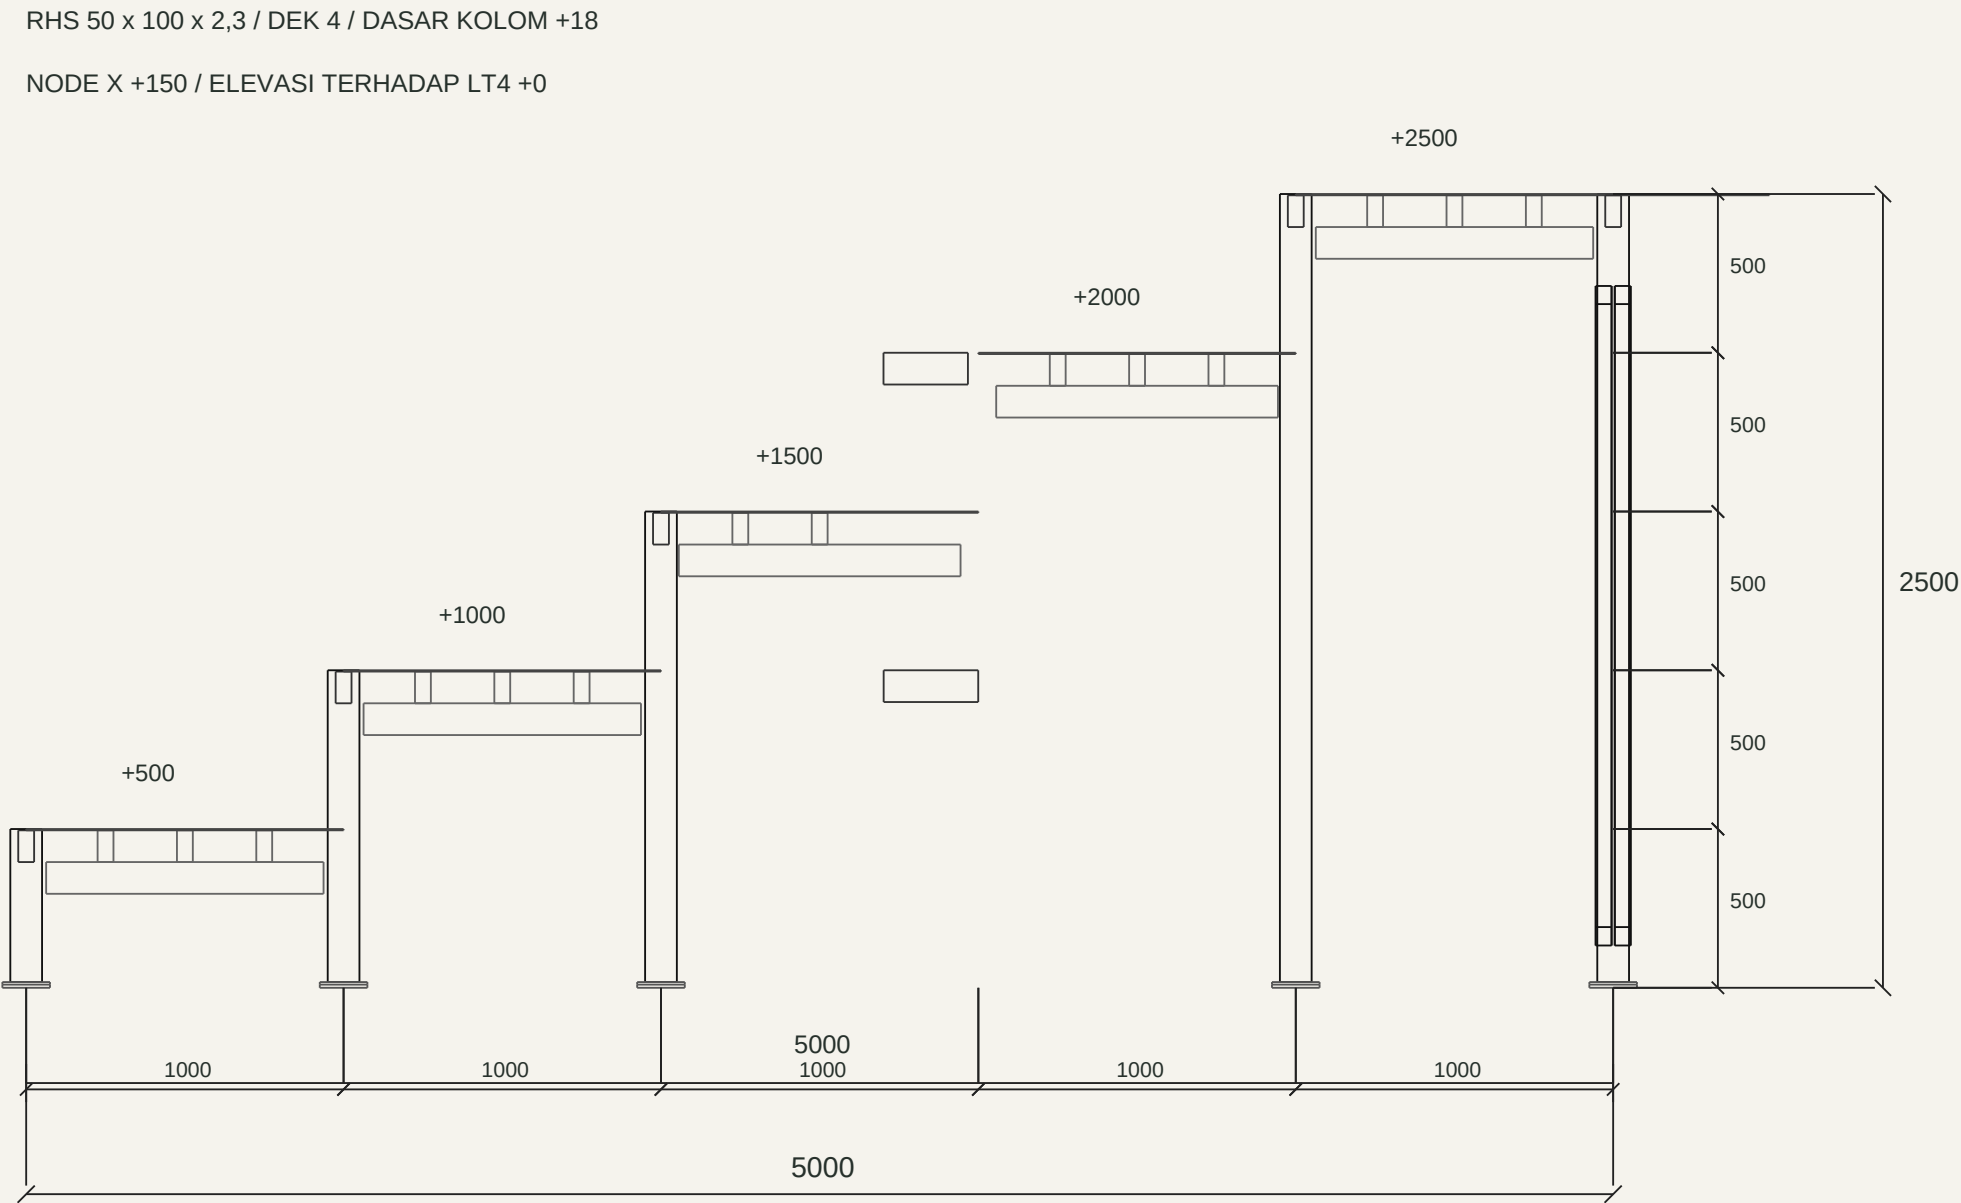


Potongan sisi x=0, toleransi seleksi 100 mm; tinggi tier nominal 500/1000/1500/2000/2500.

X melintang tetap studi. Penyaluran gaya horizontal ke beton belum terverifikasi.

LOD 200: bentuk, ukuran dan posisi perkiraan. Detail sambungan mengikuti status masing-masing.

SATUAN: mm | PDF: FIT / NTS | DIMENSI NOMINAL KOORDINASI | DETAIL TERSEDIA DIPERTAHANKAN

S-06 POTONGAN PORTAL

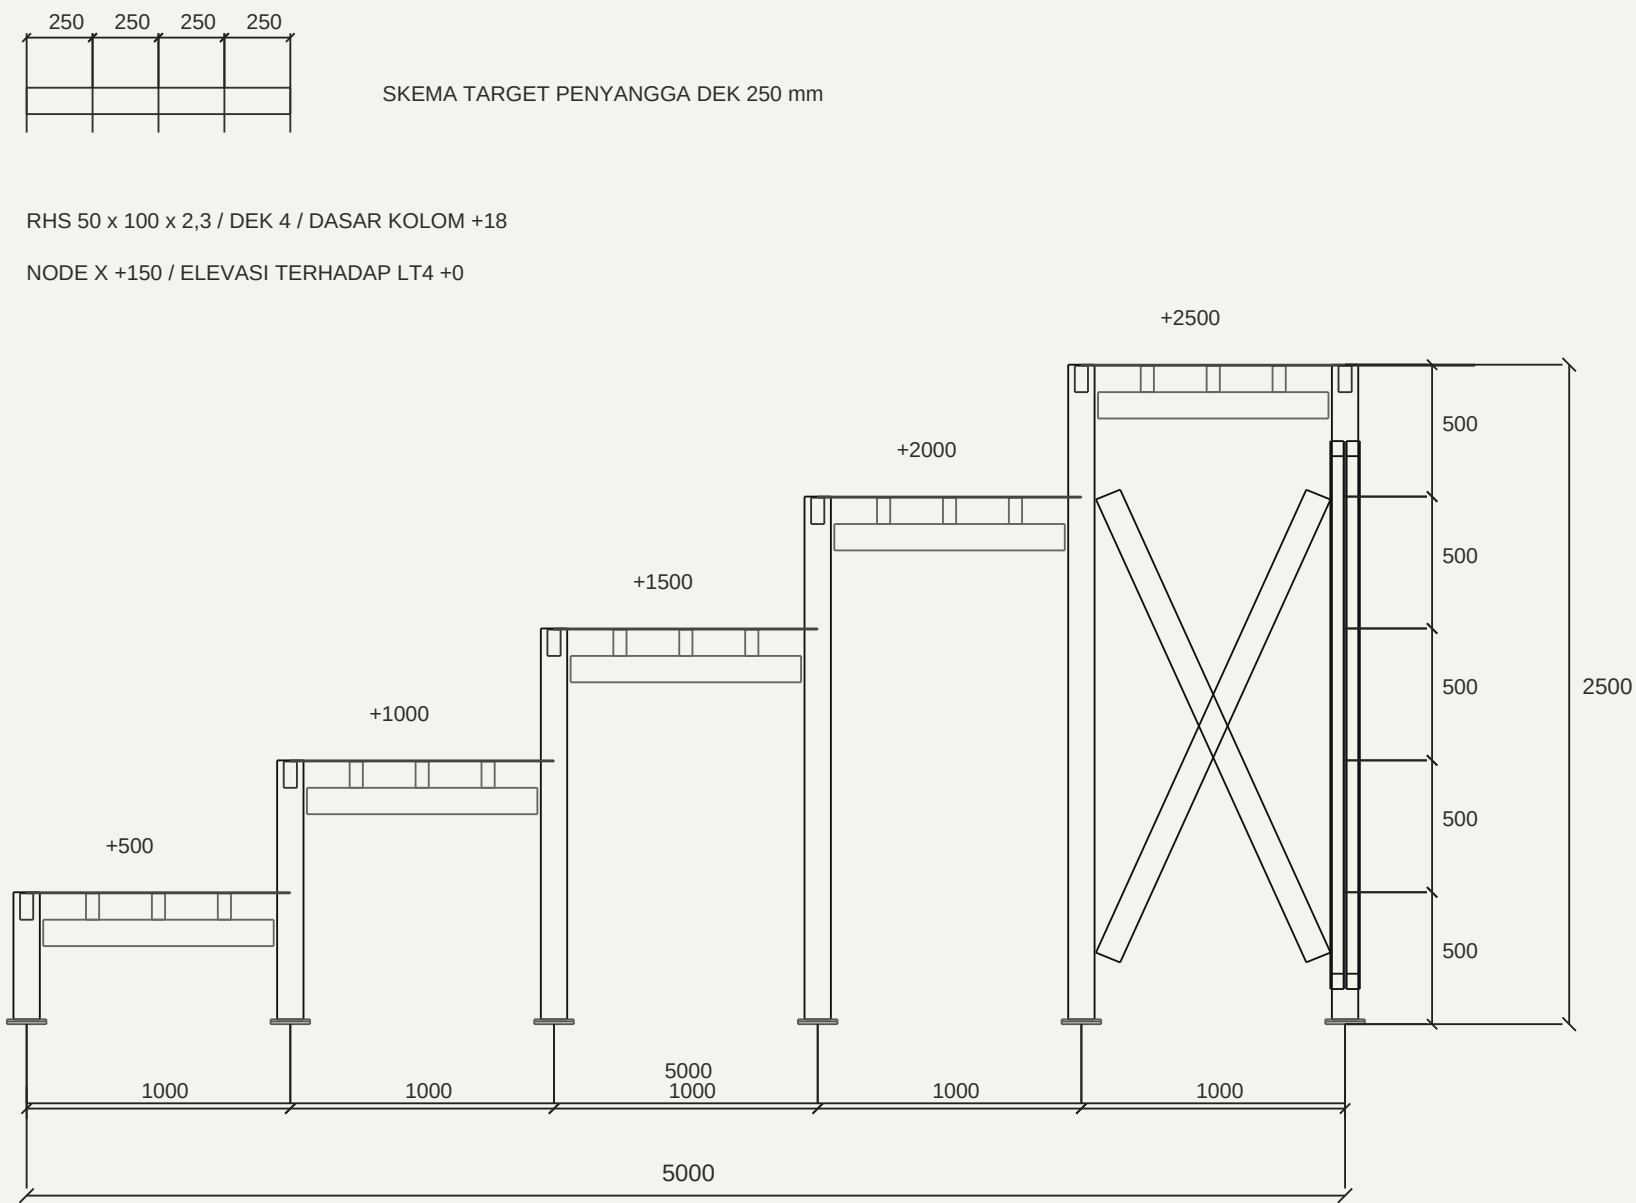

Potongan portal x=1770, toleransi seleksi 100 mm. Dek 4 mm; tumpuan utama mengikuti model.

Jarak penyangga 250 mm adalah target studi dek, bukan bukti beban titik dan getaran lurus.


LOD 200: bentuk, ukuran dan posisi perkiraan. Detail sambungan mengikuti status masing-masing.

SATUAN: mm | PDF: FIT / NTS | DIMENSI NOMINAL KOORDINASI | DETAIL TERSEDIA DIPERTAHANKAN

S-07 POTONGAN TANGGA

5 MODUL x 1000 / 15 KENAIKAN x 166,67 (NOMINAL)

BORDES 4 mm / USULAN KOORDINASI

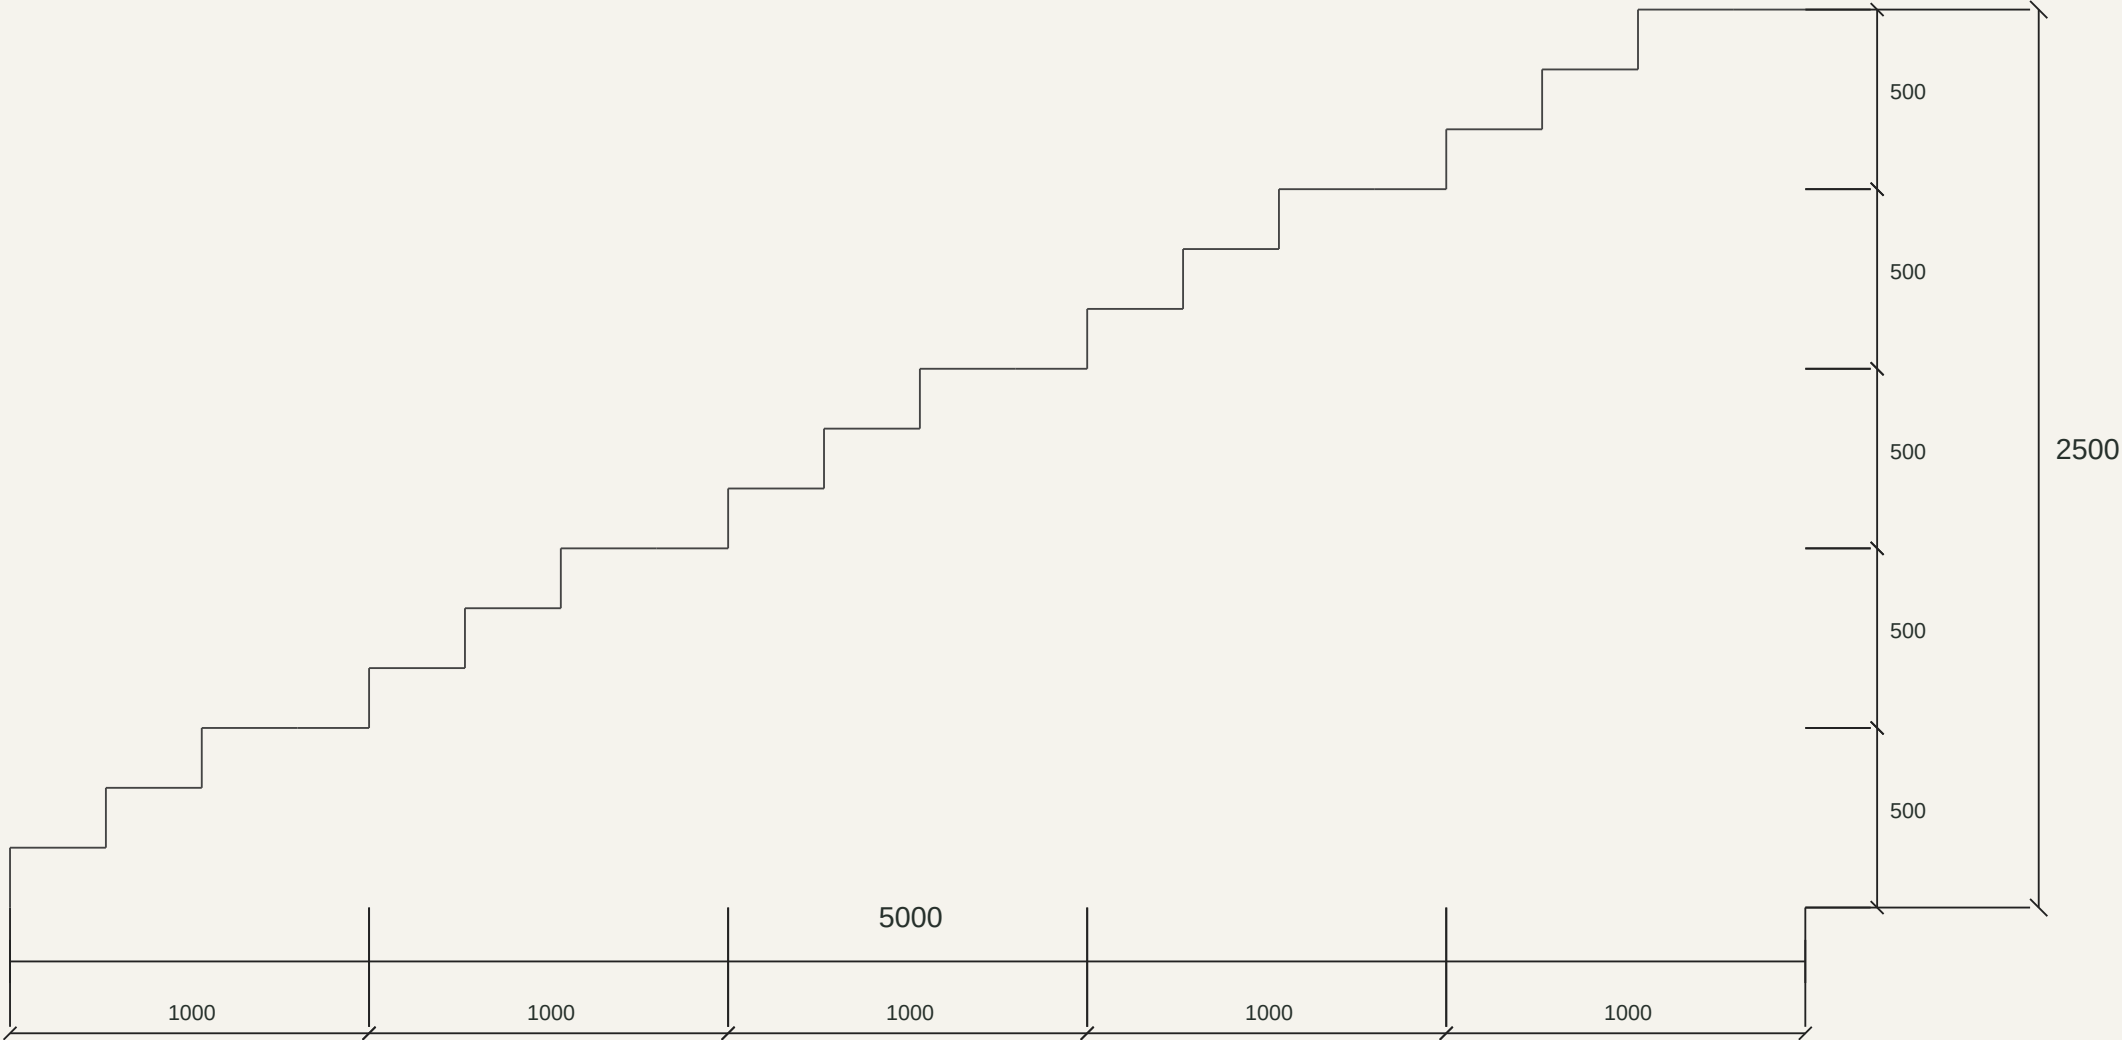


Geometri tangga dari web arsitektur; 5 tier, kenaikan per tier 500 mm.
Jalur 2000 mm terpotong kolom beton; jalur 600 mm belum dibuktikan memenuhi evakuasi.
LOD 200: bentuk, ukuran dan posisi perkiraan. Detail sambungan mengikuti status masing-masing.

S-08 DETAIL ANAK TANGGA

TAPAK 267 / LANDING 199 / DEK 4 mm

Radius tekuk dan panjang bentangan: belum ditetapkan
BORDES 4 mm / USULAN KOORDINASI

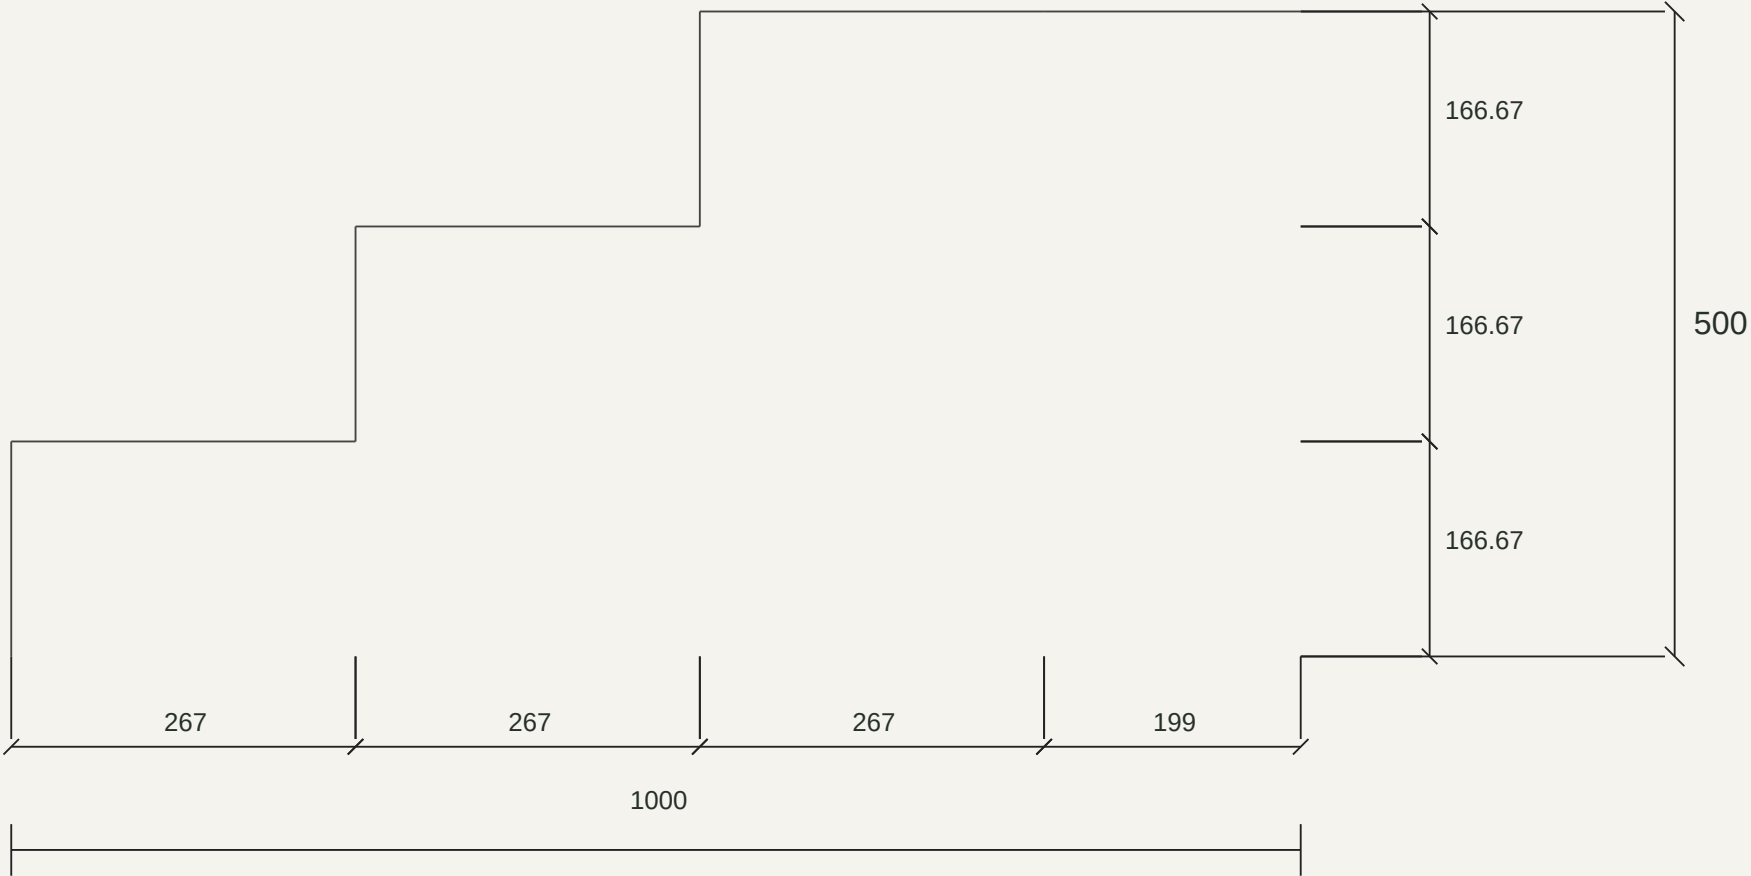

Satu modul usulan: 3 kenaikan 166,67 mm; tapak 267 mm, sisa landing 199 mm.


Bordes 4 mm. Radius tekuk, bentangan potong dan rangka tangga belum ditetapkan.

LOD 200: bentuk, ukuran dan posisi perkiraan. Detail sambungan mengikuti status masing-masing.

SATUAN: mm | PDF: FIT / NTS | DIMENSI NOMINAL KOORDINASI | DETAIL TERSEDIA DIPERTAHANKAN

S-09 RAILING & BALUSTRADE

RAILING SKEMATIS; PROFIL PADA MODEL DIPERTAHANKAN

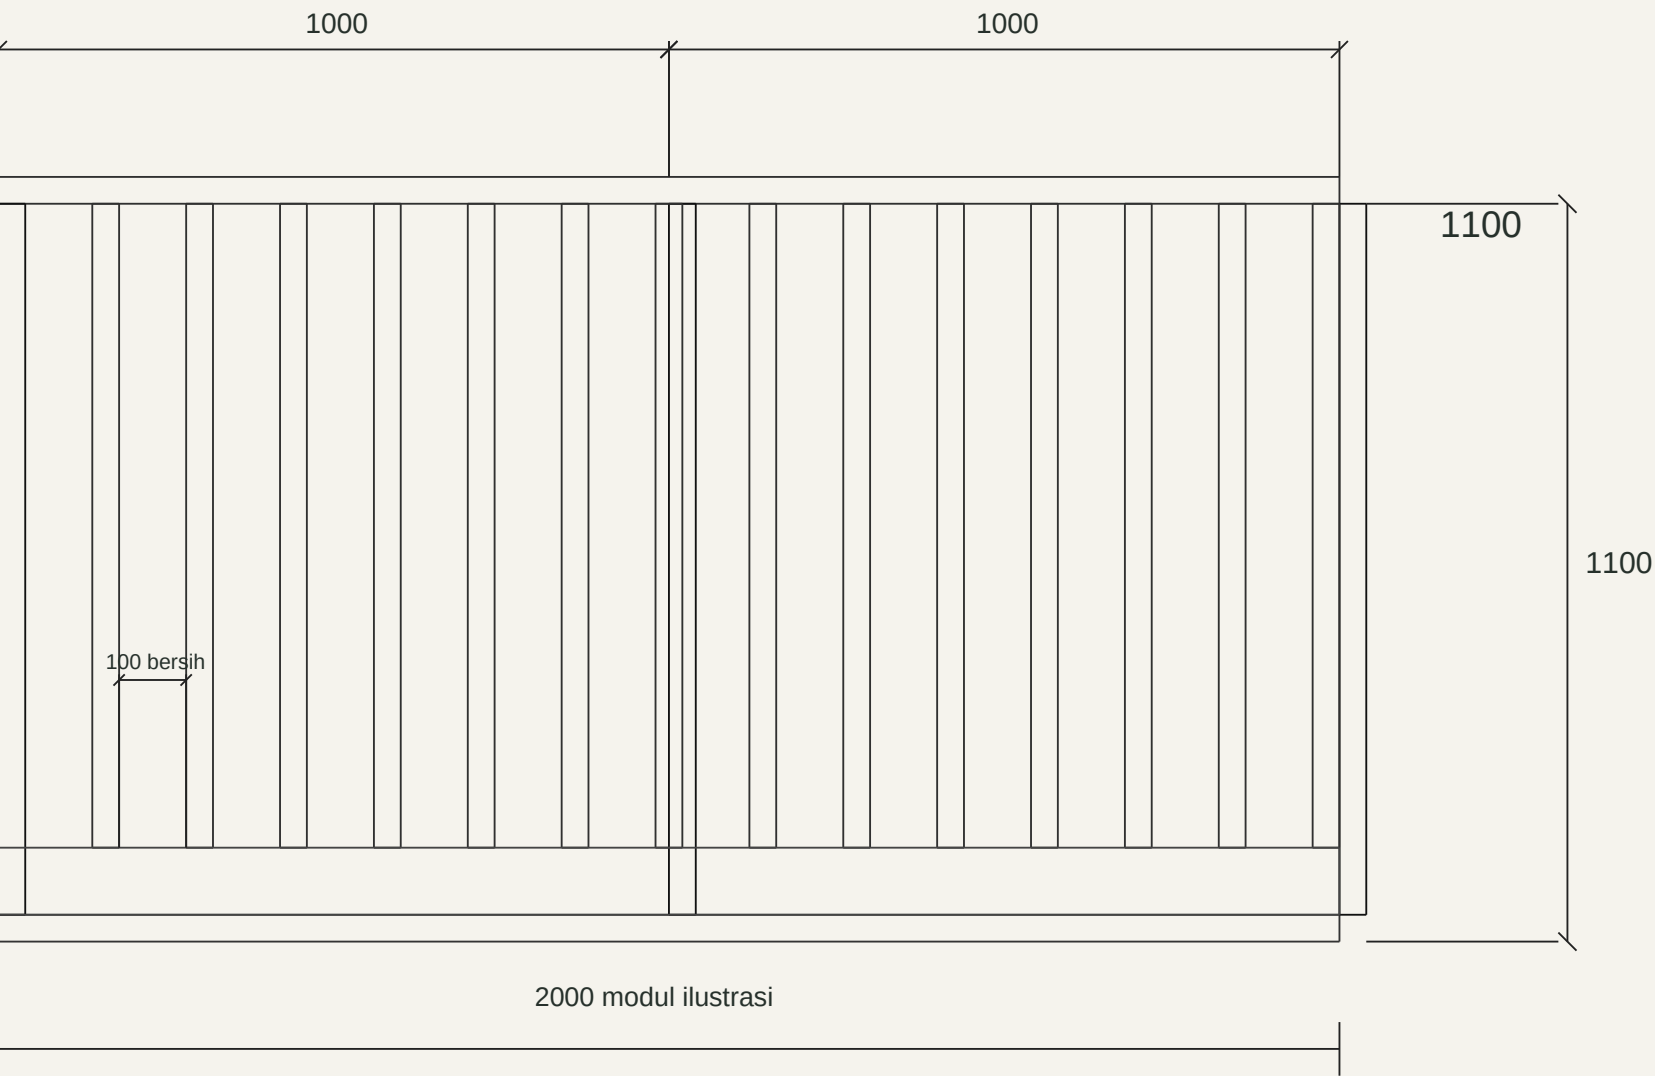

Skema koordinasi: tinggi 1100 mm, bukaan bersih baluster <=100 mm sebagai target studi.


Beban pagar, pemanjatan, sambungan dan lebar jalur harus diperiksa; ukuran bukan persetujuan.

LOD 200: bentuk, ukuran dan posisi perkiraan. Detail sambungan mengikuti status masing-masing.


SATUAN: mm | PDF: FIT / NTS | DIMENSI NOMINAL KOORDINASI | DETAIL TERSEDIA DIPERTAHANKAN

S-10 BASE PLATE & KARET

RHS 50 x 100 x 2,3 / DIMENSI NOMINAL

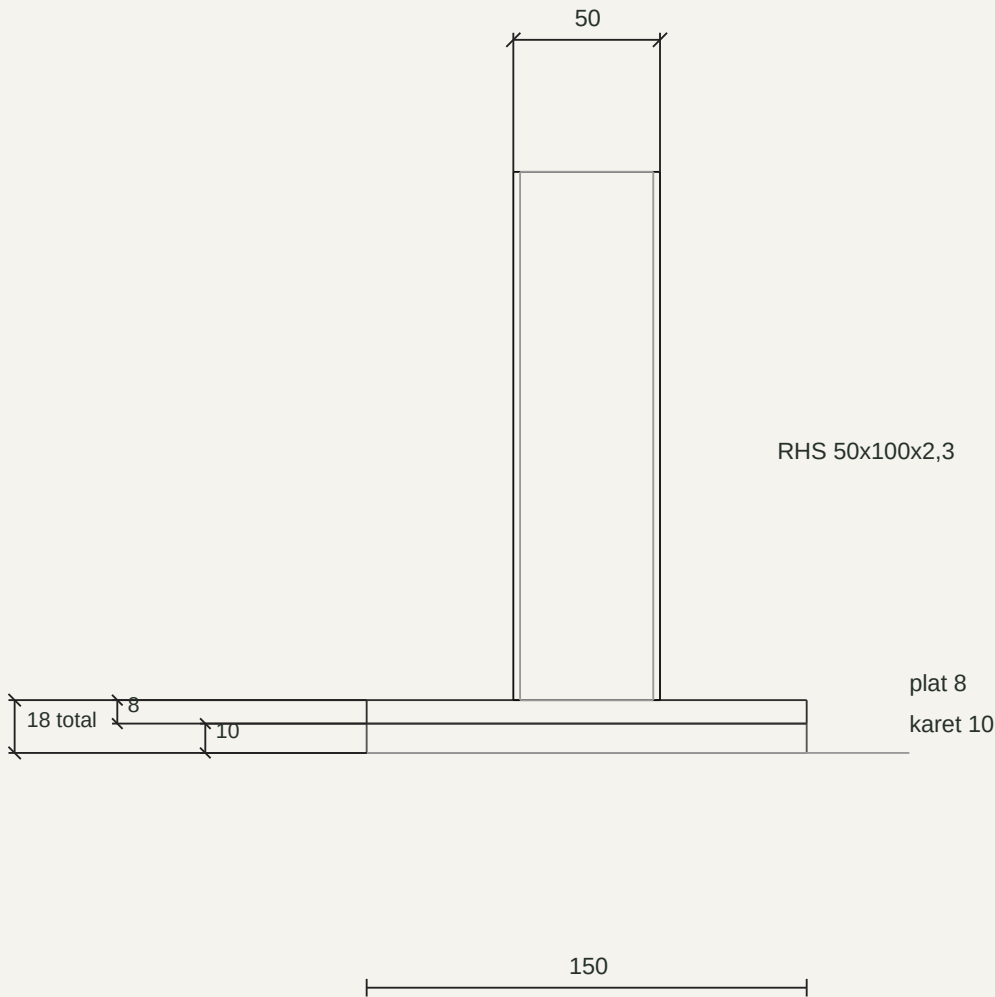

DENAH DUDUKAN

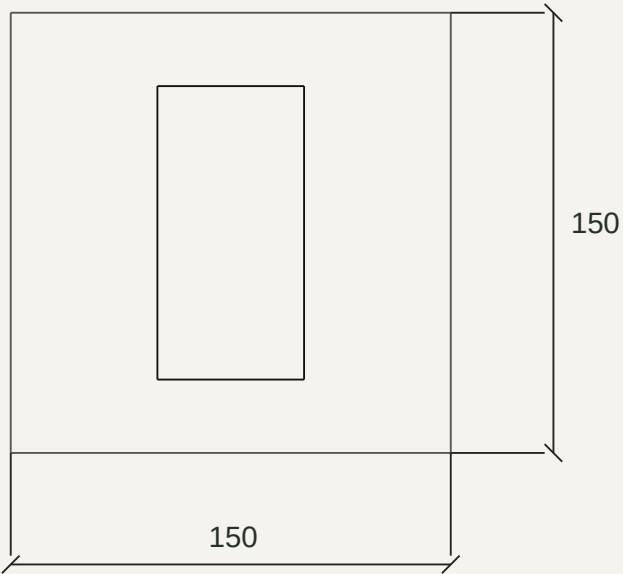

PLAT 150 x 150 x 8

KARET 150 x 150 x 10

Dudukan sesuai model: karet 10, base plate 8, kolom mulai +18 mm.

Tanpa angkur ke pelat LT4 mengikuti konsep sumber. Las dan tahan geser/angkat belum dirancang.


LOD 200: bentuk, ukuran dan posisi perkiraan. Detail sambungan mengikuti status masing-masing.

SATUAN: mm | PDF: FIT / NTS | DIMENSI NOMINAL KOORDINASI | DETAIL TERSEDIA DIPERTAHANKAN

S-11 SAMBUNGAN D1-D4


PENAMPANG RHS RUJUKAN; SKEMA D1-D4 TIDAK DIUKUR UNTUK PRODUKSI

D3 / IKATAN BETON

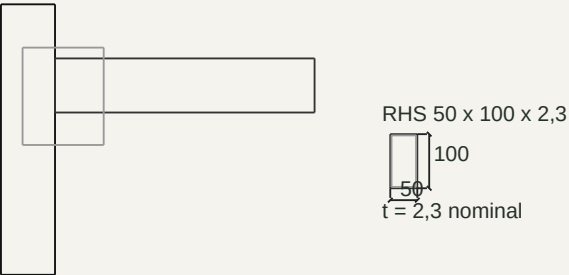


UKURAN SAMBUNGAN: HOLD

D4 / RAILING-RANGKA

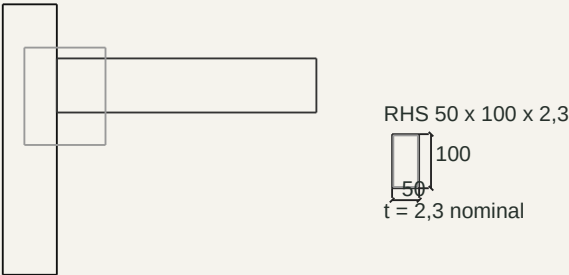


UKURAN SAMBUNGAN: HOLD

D1 / BALOK-KOLOM

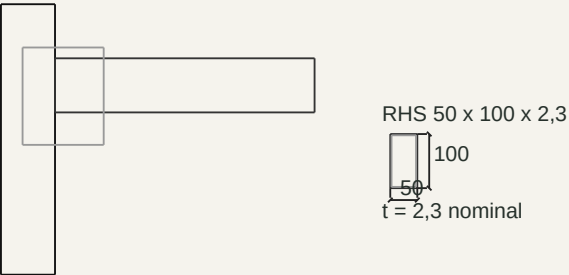

UKURAN SAMBUNGAN: HOLD

D2 / X-KOLOM

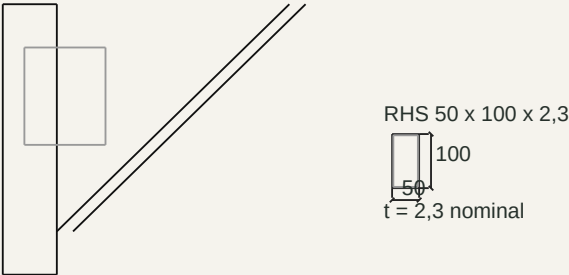

UKURAN SAMBUNGAN: HOLD

Baut, angkur, gusset dan ukuran las: belum ditetapkan


D1 balok-kolom; D2 X-kolom; D3 ikatan ke beton; D4 railing-rangka.

Skema jalur gaya saja. Diameter baut, las, gusset dan angkur lama tidak berlaku otomatis.

LOD 200: bentuk, ukuran dan posisi perkiraan. Detail sambungan mengikuti status masing-masing.

SATUAN: mm | PDF: FIT / NTS | DIMENSI NOMINAL KOORDINASI | DETAIL TERSEDIA DIPERTAHANKAN

S-12 URUTAN PEMASANGAN

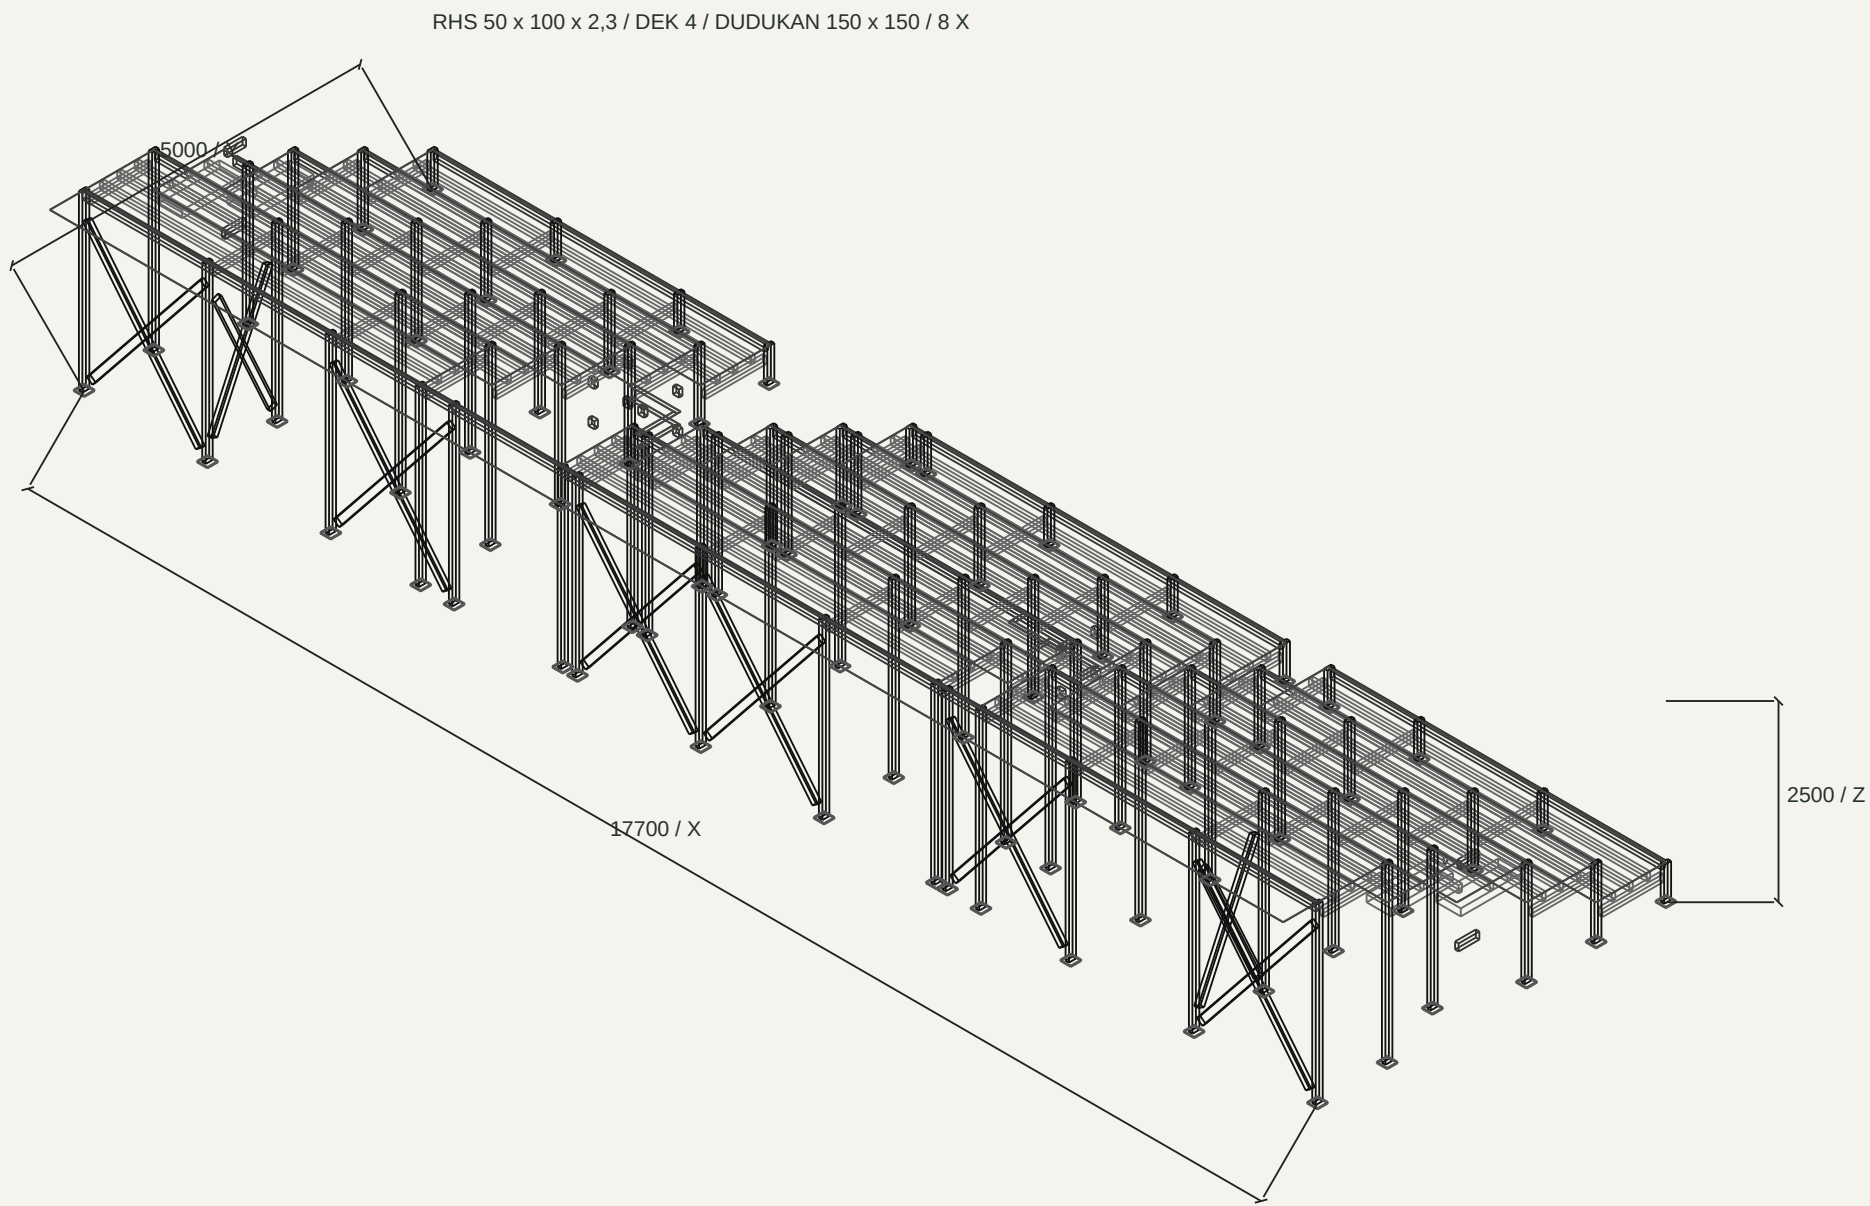

Urutan: survei beton / marking > karet & dudukan > kolom > balok & X > dek > tangga & railing.

Gunakan penyangga sementara; lepas setelah stabilitas dan semua sambungan diperiksa.

LOD 200: bentuk, ukuran dan posisi perkiraan. Detail sambungan mengikuti status masing-masing.

SATUAN: mm | PDF: FIT / NTS | DIMENSI NOMINAL KOORDINASI | DETAIL TERSEDIA DIPERTAHANKAN