



S-01 DENAH TRIBUN

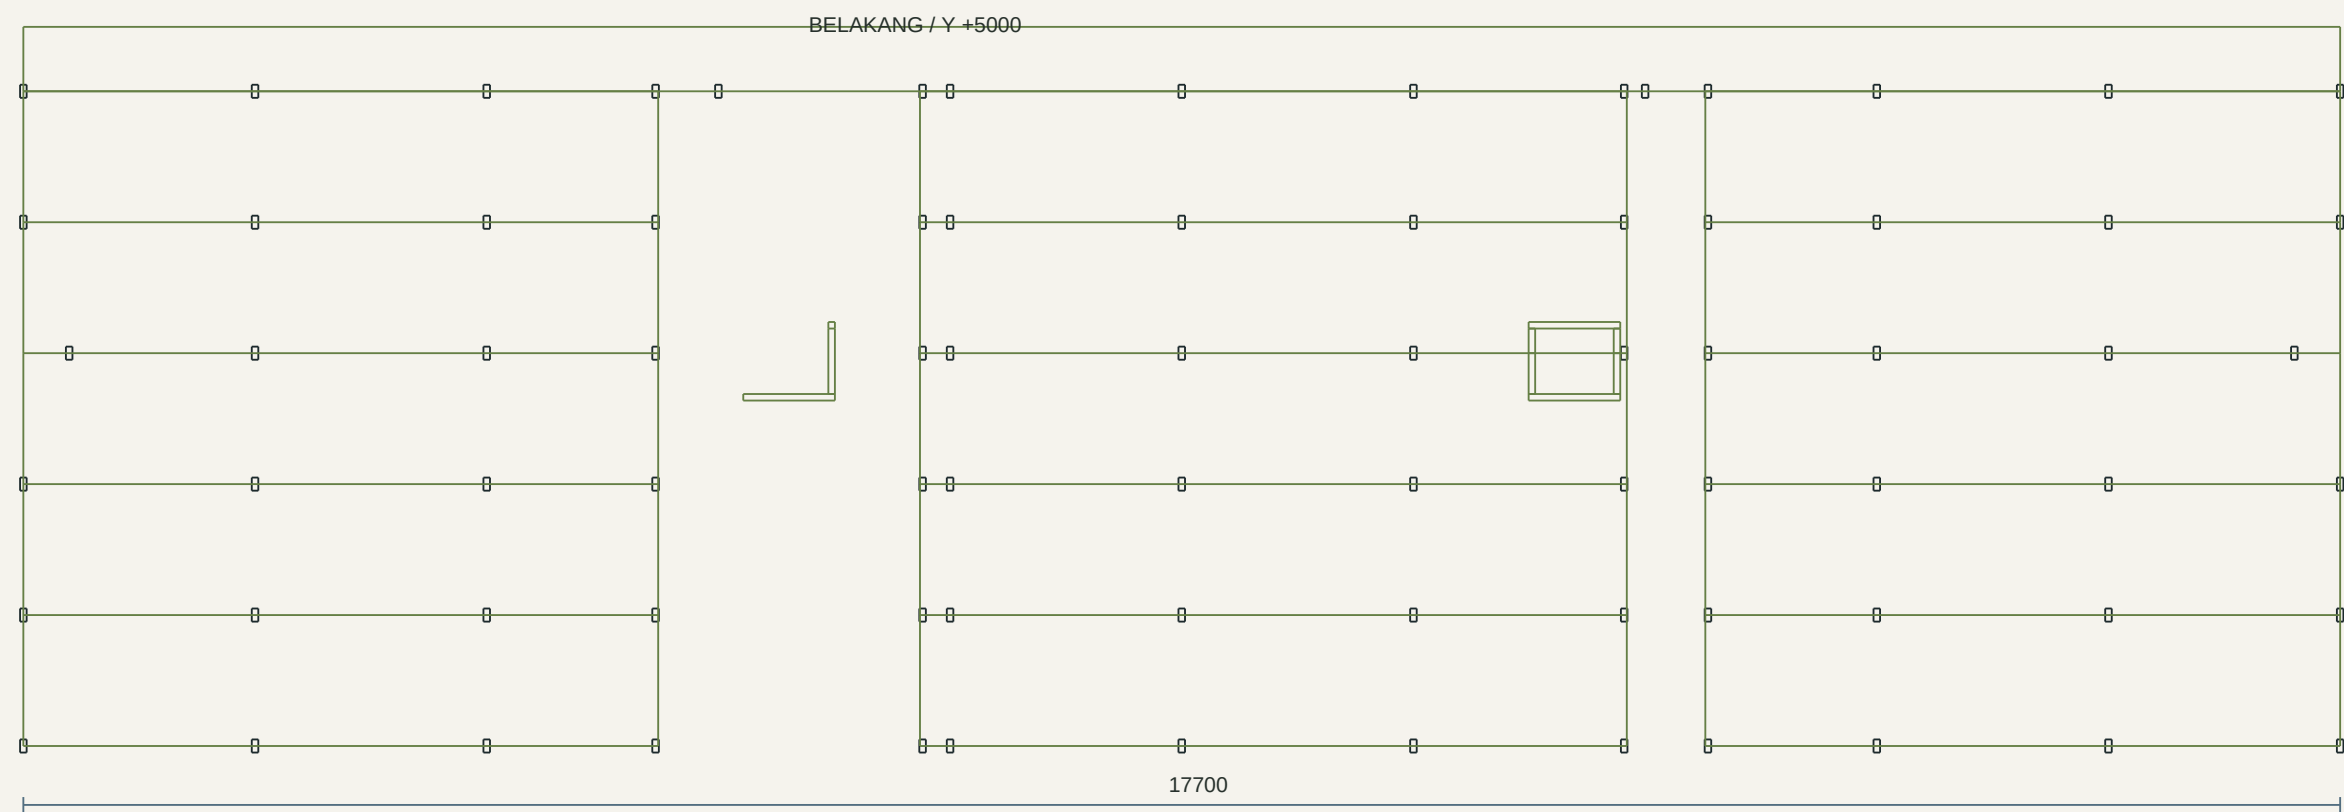


Dek bordes 4 mm. Proyeksi batas luar model; bukaan di sekitar beton harus disurvei.

Area BOQ 82,345 m2 dari parameter Revit; bukan luas proyeksi persegi gambar ini.

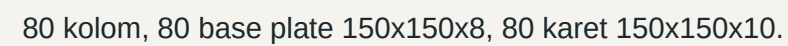

SATUAN DXF: mm | PDF: FIT / NTS | DIMENSI TERTULIS YANG BERLAKU | BUKAN UNTUK FABRIKASI

S-03 RENCANA RANGKA & X

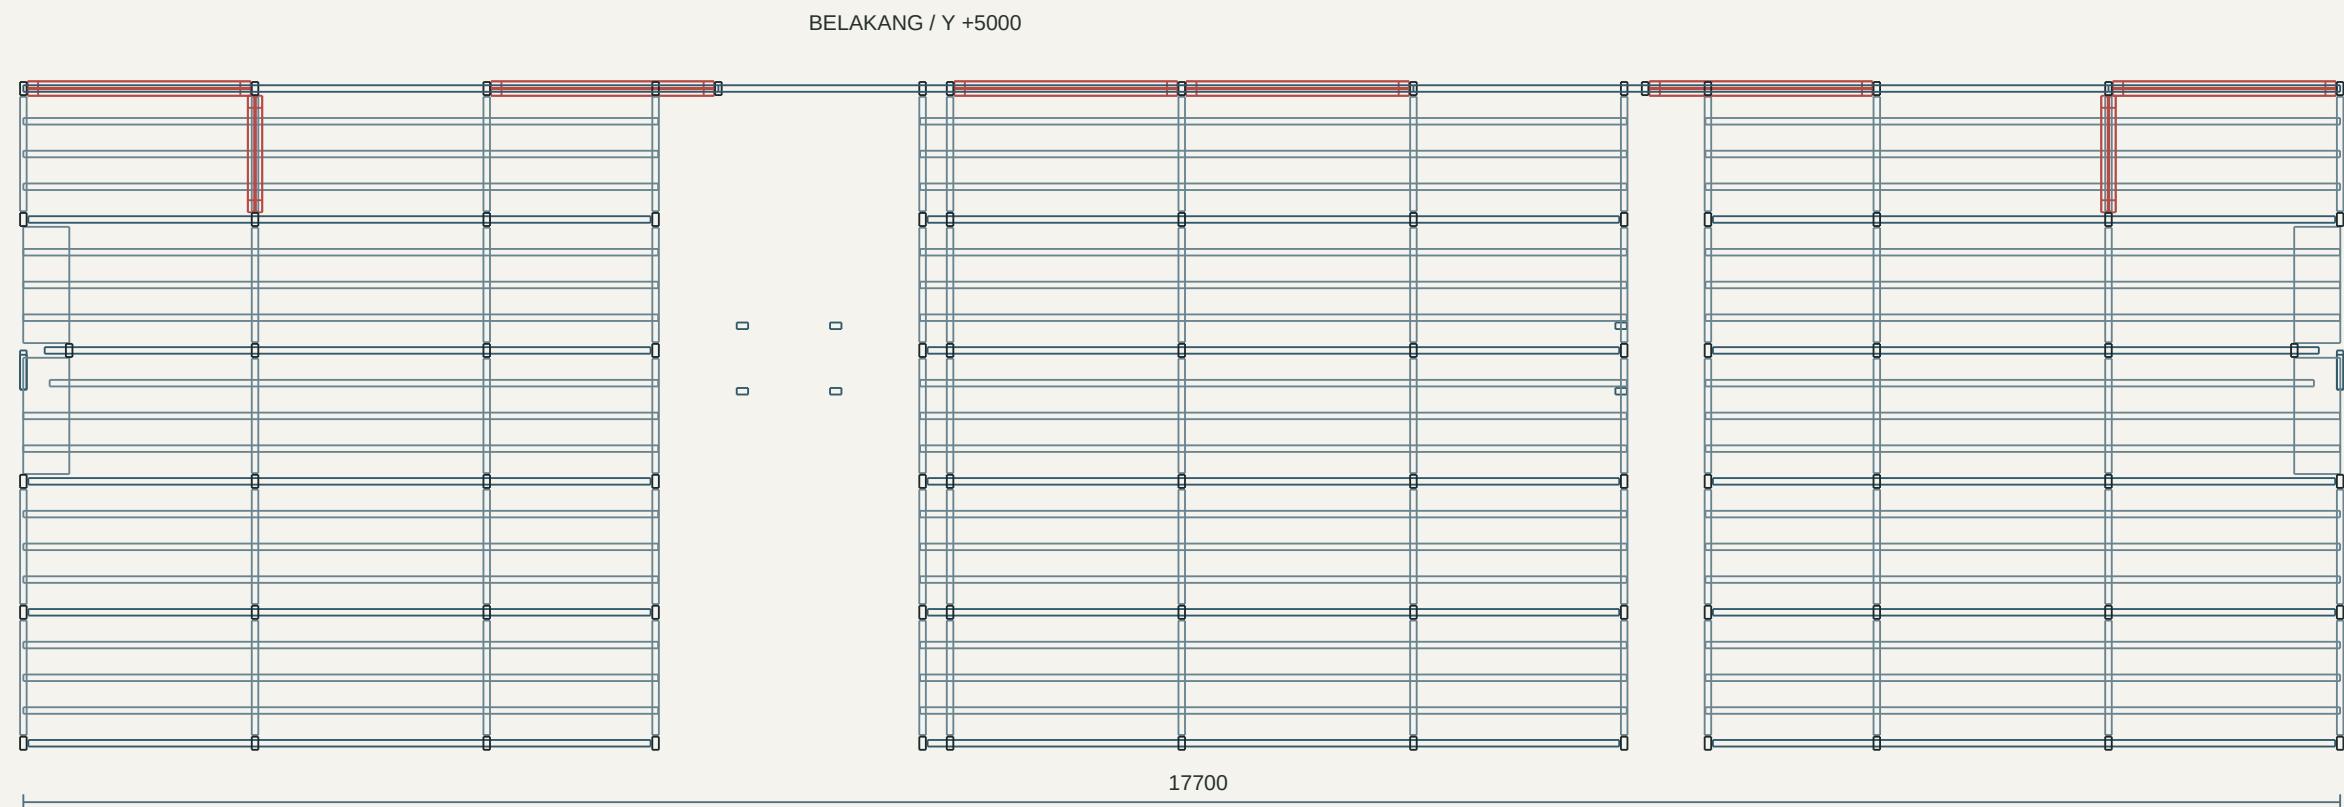


161 RHS 50x100x2,3 termasuk 16 diagonal / 8 X. Node bawah +150 mm.
45 joist longitudinal dan 65 balok silang mengikuti revisi model; celah sambungan belum final.

S-04 TAMPAK DEPAN



Proyeksi rangka dari lapangan. Semua tingkat terlihat transparan; garis belakang tidak dihapus.
Finishing, railing dan tangga perlu dicocokkan dengan model arsitektur.


S-05 TAMPAK SAMPING

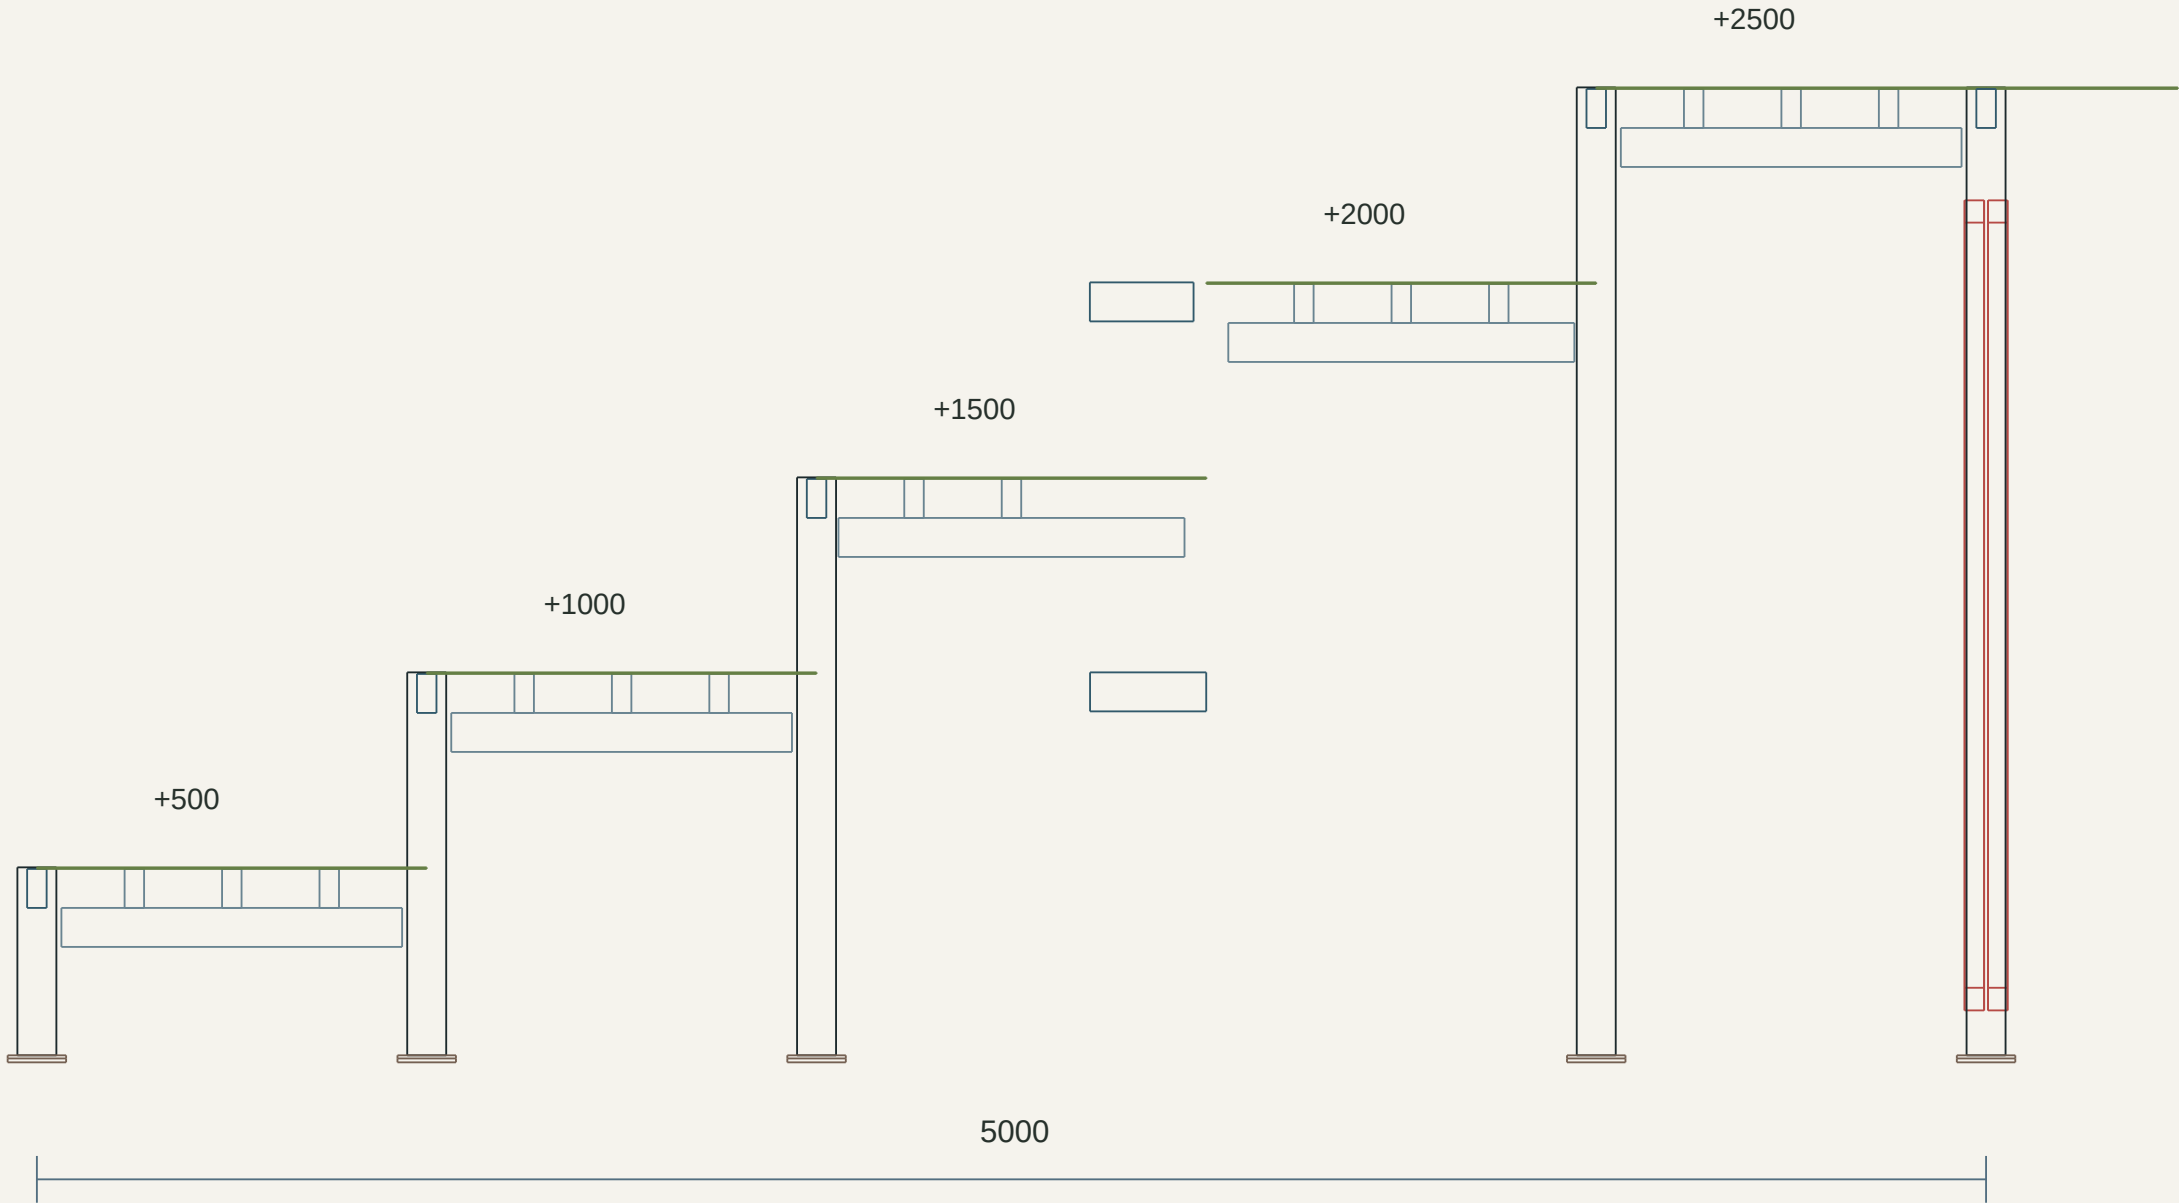

Potongan sisi x=0, toleransi seleksi 100 mm; tinggi tier nominal 500/1000/1500/2000/2500.

X melintang tetap studi. Penyaluran gaya horizontal ke beton belum terverifikasi.

S-06 POTONGAN PORTAL

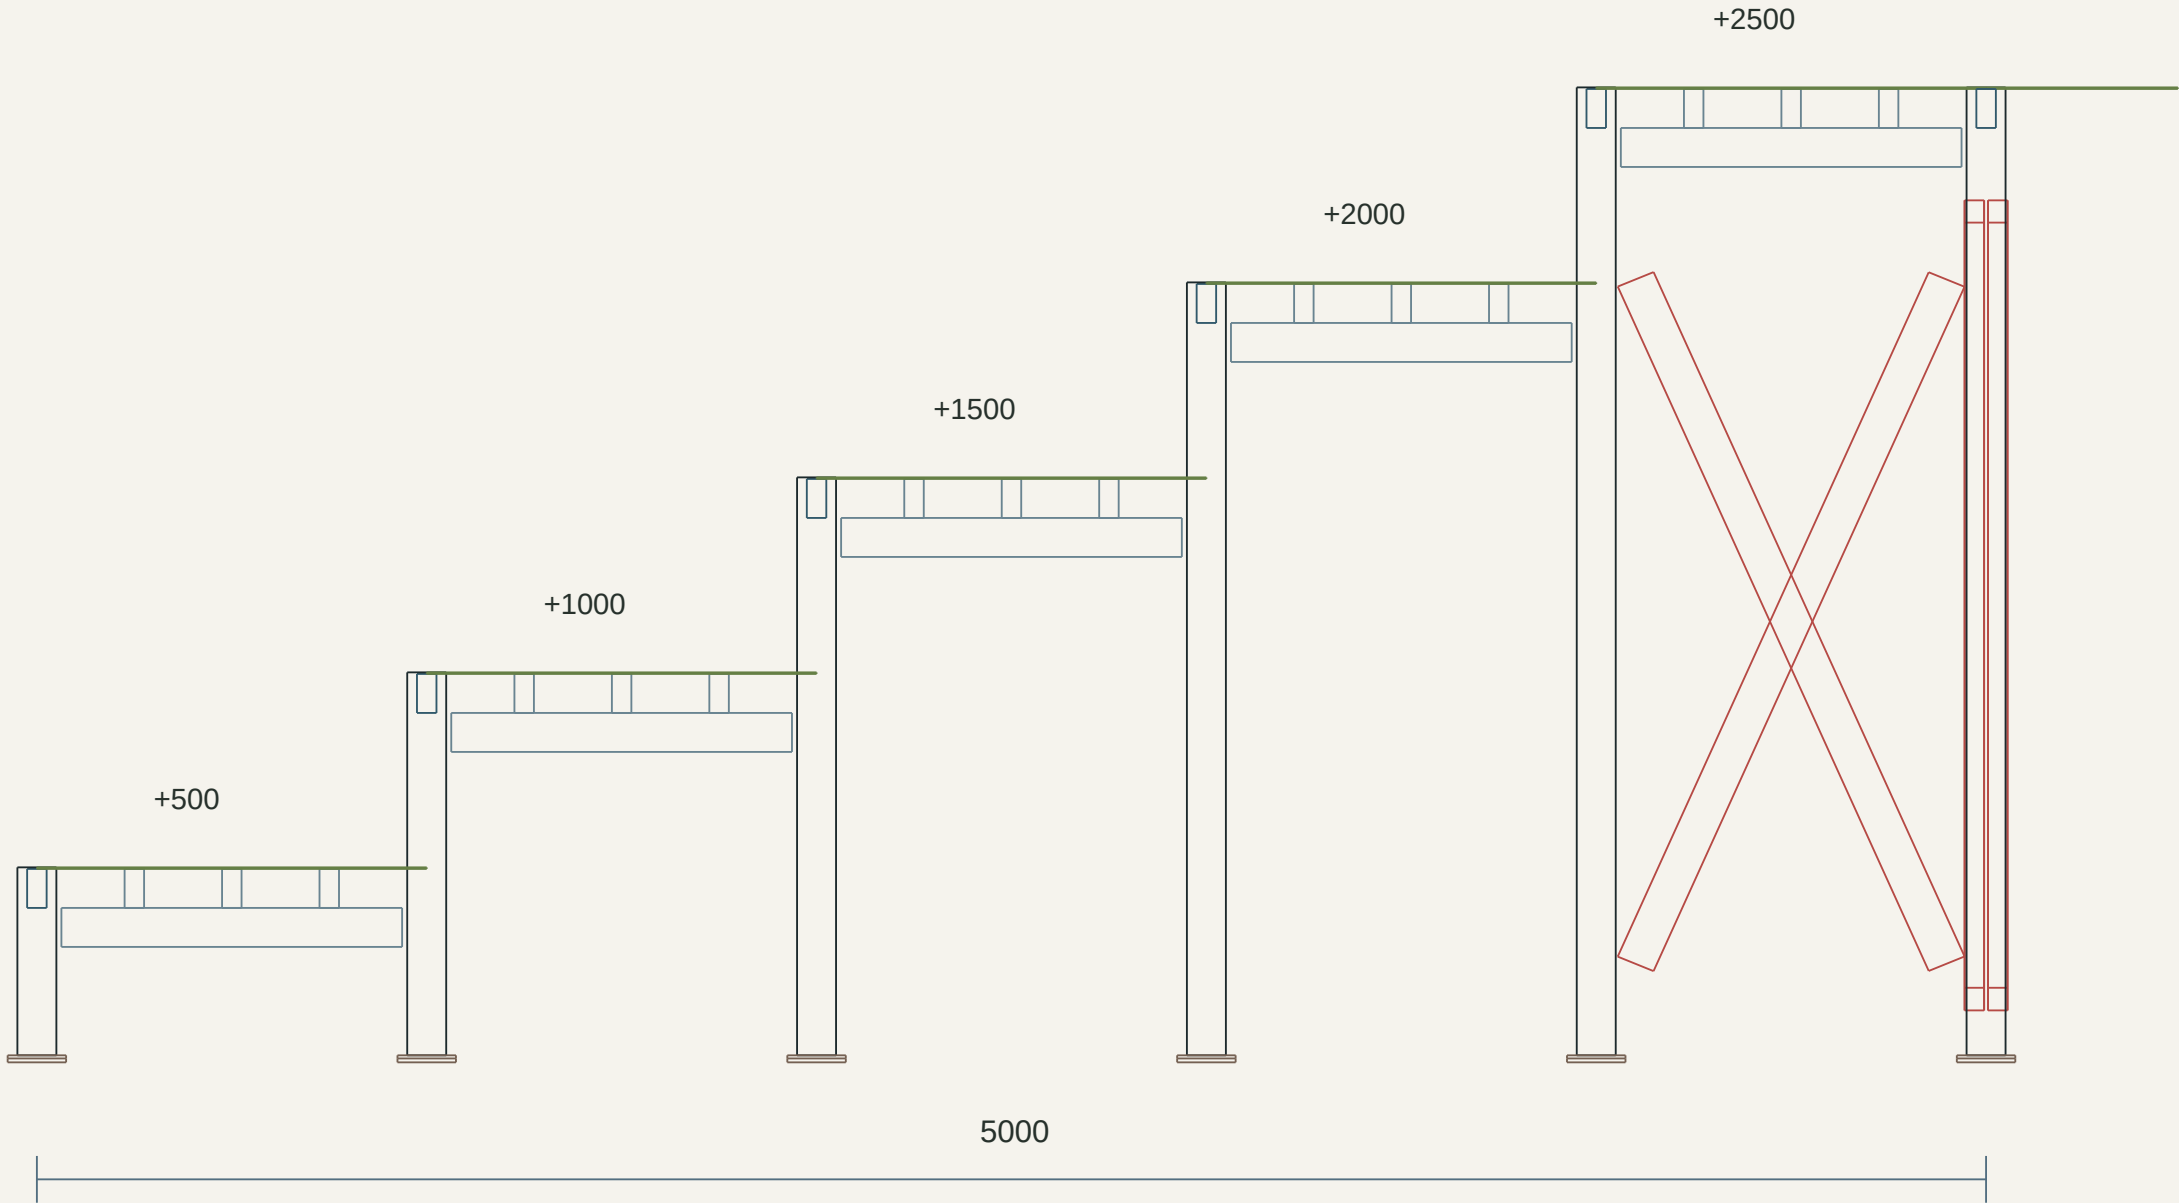


Potongan portal x=1770, toleransi seleksi 100 mm. Dek 4 mm; tumpuan utama mengikuti model.

Jarak penyangga 250 mm adalah target studi dek, bukan bukti beban titik dan getaran lurus.

S-07 POTONGAN TANGGA

KOORDINASI

BORDES 4 mm / USULAN KOORDINASI

 


Geometri tangga dari web arsitektur; 5 tier, kenaikan per tier 500 mm.
Jalur 2000 mm terpotong kolom beton; jalur 600 mm belum dibuktikan memenuhi evakuasi.

S-08 DETAIL ANAK TANGGA

KOORDINASI


BORDES 4 mm / USULAN KOORDINASI

 

Satu modul usulan: 3 kenaikan 166,67 mm; tapak 267 mm, sisa landing 199 mm.


Bordes 4 mm. Radius tekuk, bentangan potong dan rangka tangga belum ditetapkan.

S-09 RAILING & BALUSTRADE

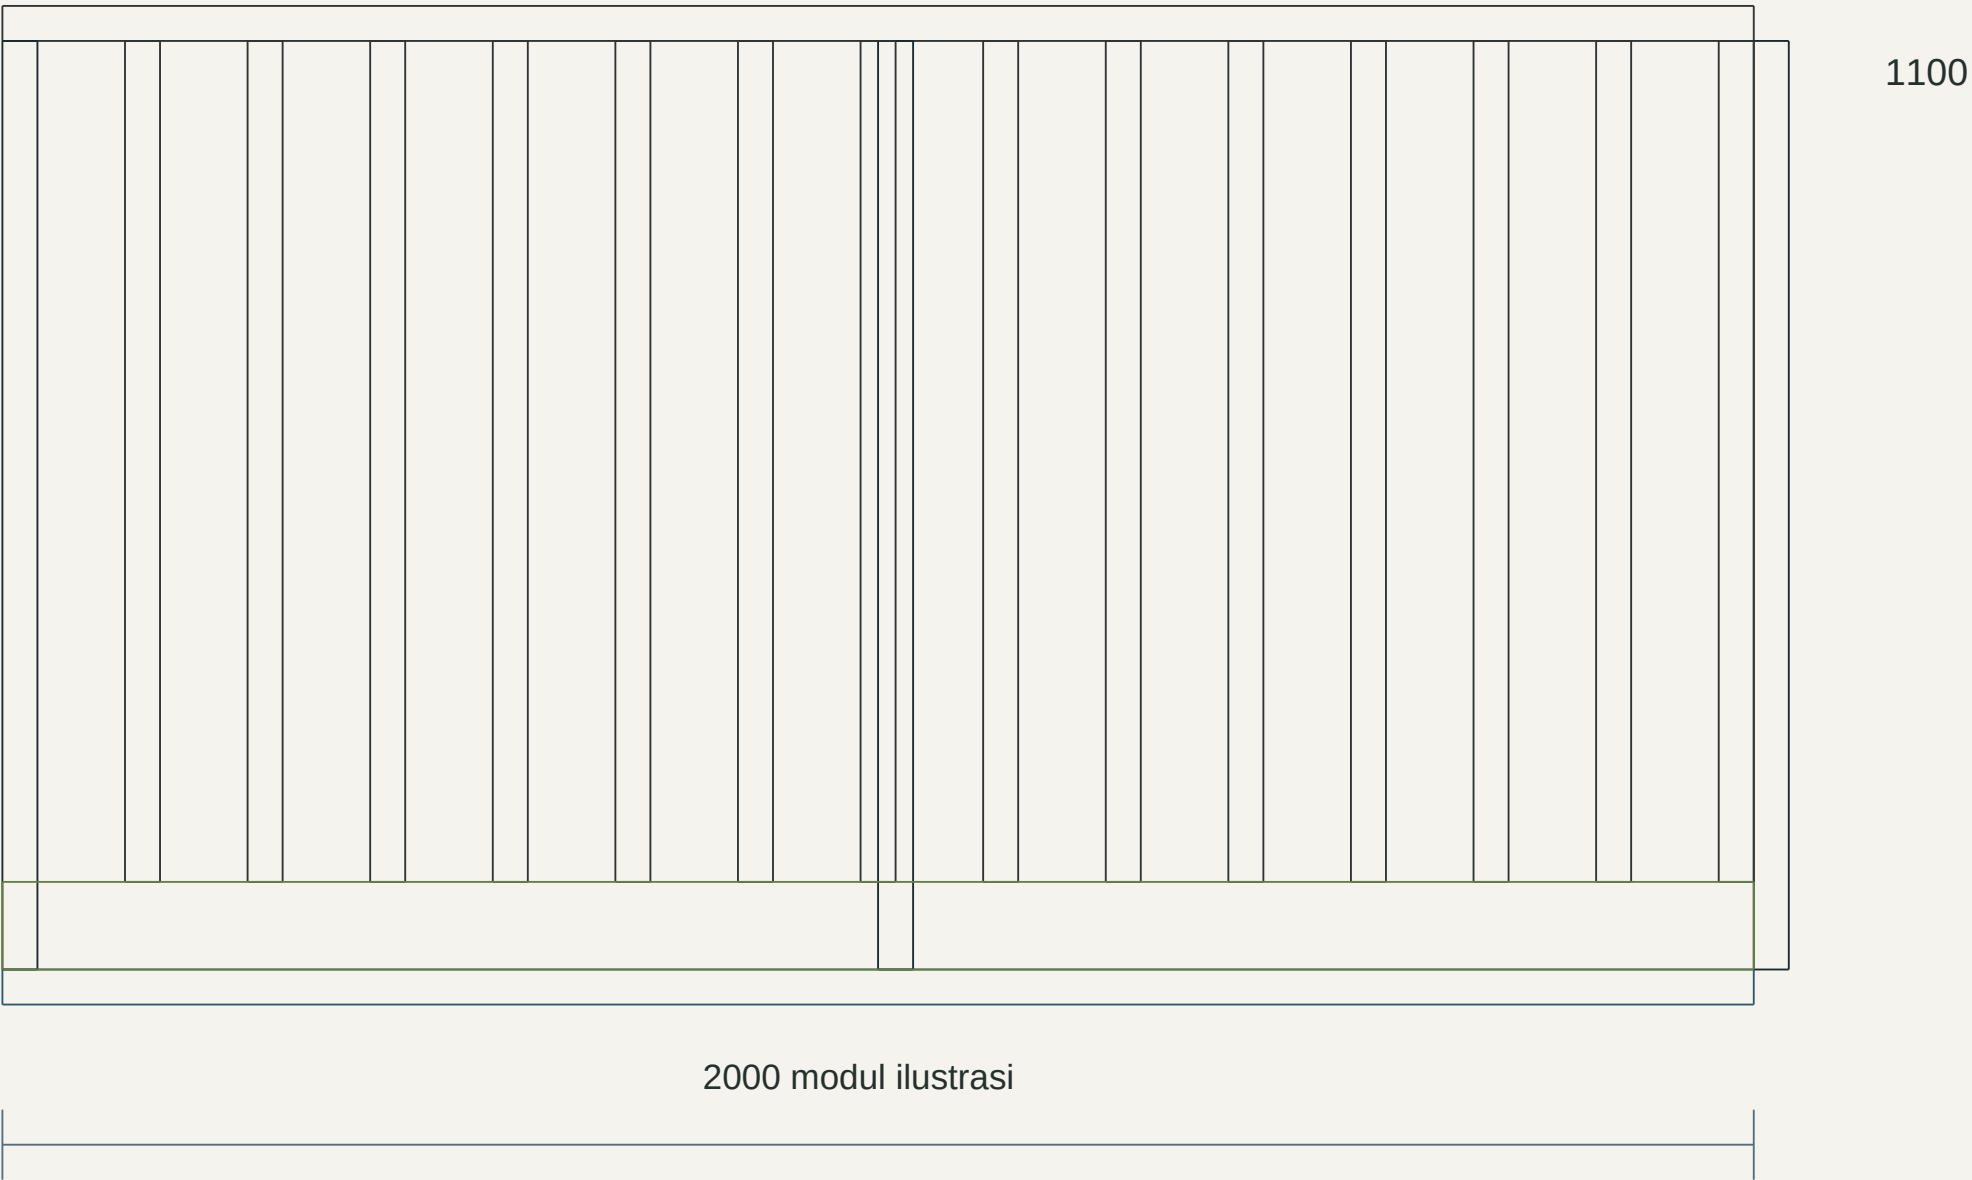

Skema koordinasi: tinggi 1100 mm, bukaan bersih baluster <=100 mm sebagai target studi.
Beban pagar, pemanjatan, sambungan dan lebar jalur harus diperiksa; ukuran bukan persetujuan.


S-10 BASE PLATE & KARET

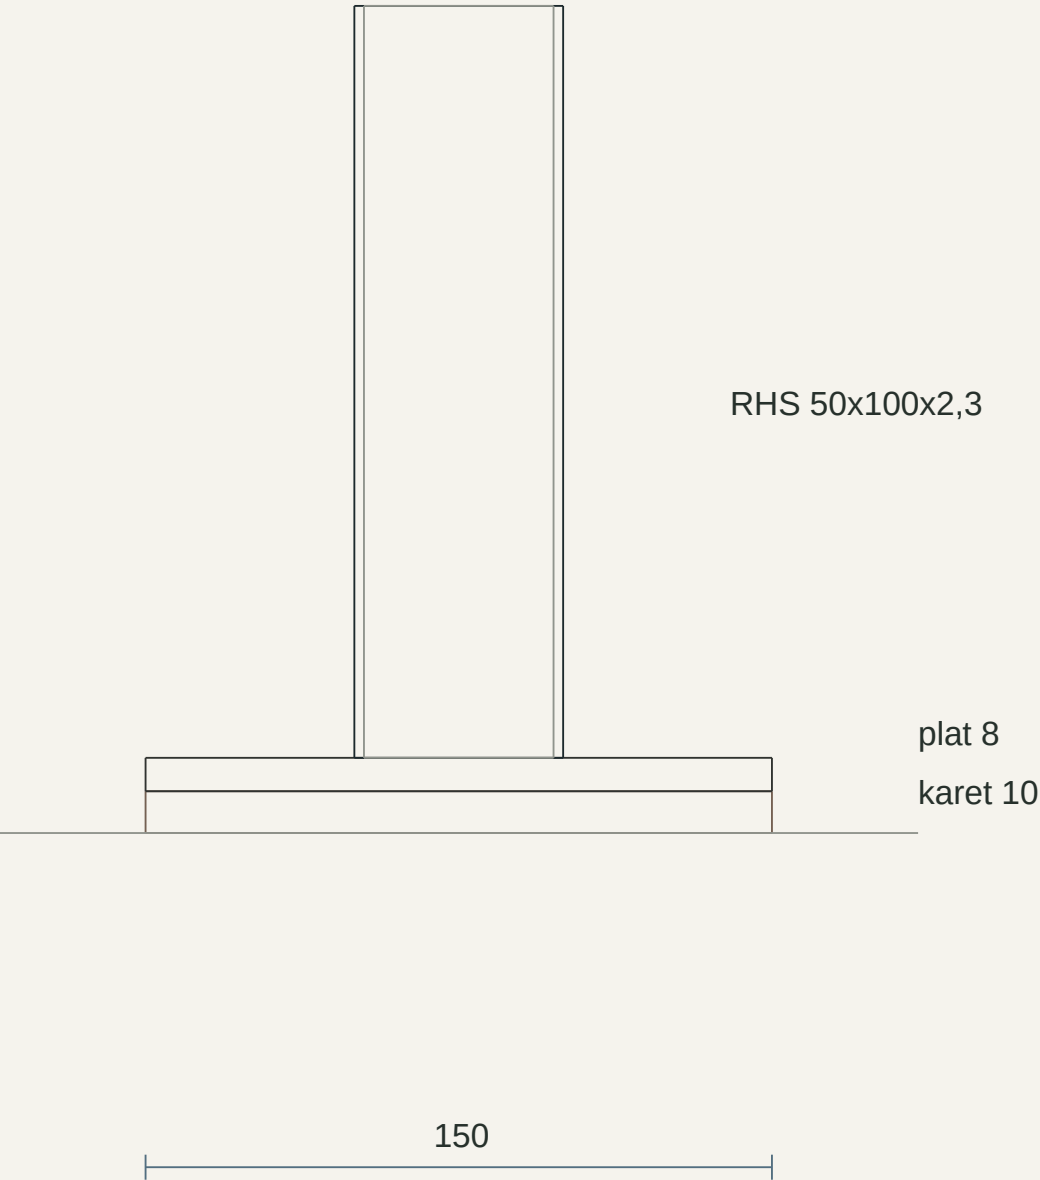

Dudukan sesuai model: karet 10, base plate 8, kolom mulai +18 mm.
Tanpa angkur ke pelat LT4 mengikuti konsep sumber. Las dan tahan geser/angkat belum dirancang.


S-11 SAMBUNGAN D1-D4

D3 / IKATAN BETON

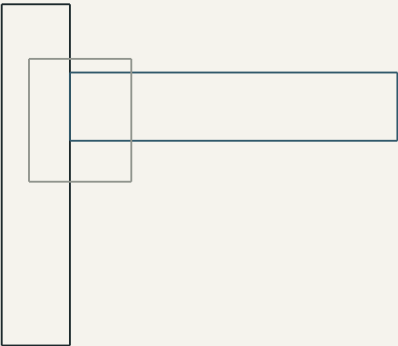


UKURAN SAMBUNGAN: HOLD

D4 / RAILING-RANGKA

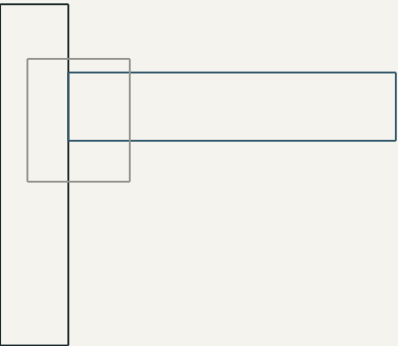


UKURAN SAMBUNGAN: HOLD

D1 / BALOK-KOLOM

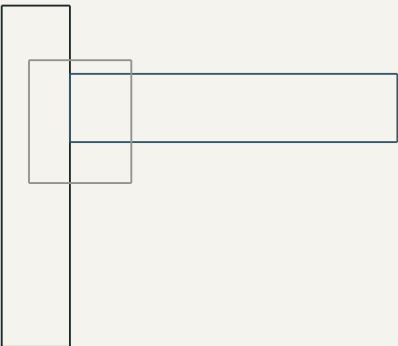

UKURAN SAMBUNGAN: HOLD


D2 / X-KOLOM

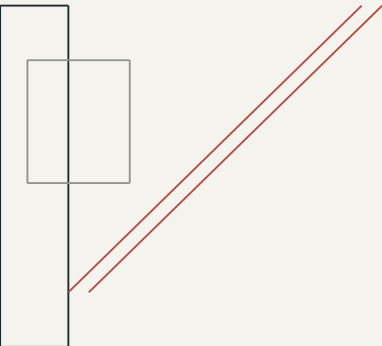

UKURAN SAMBUNGAN: HOLD

D1 balok-kolom; D2 X-kolom; D3 ikatan ke beton; D4 railing-rangka.
Skema jalur gaya saja. Diameter baut, las, gusset dan angkur lama tidak berlaku otomatis.

S-12 URUTAN PEMASANGAN

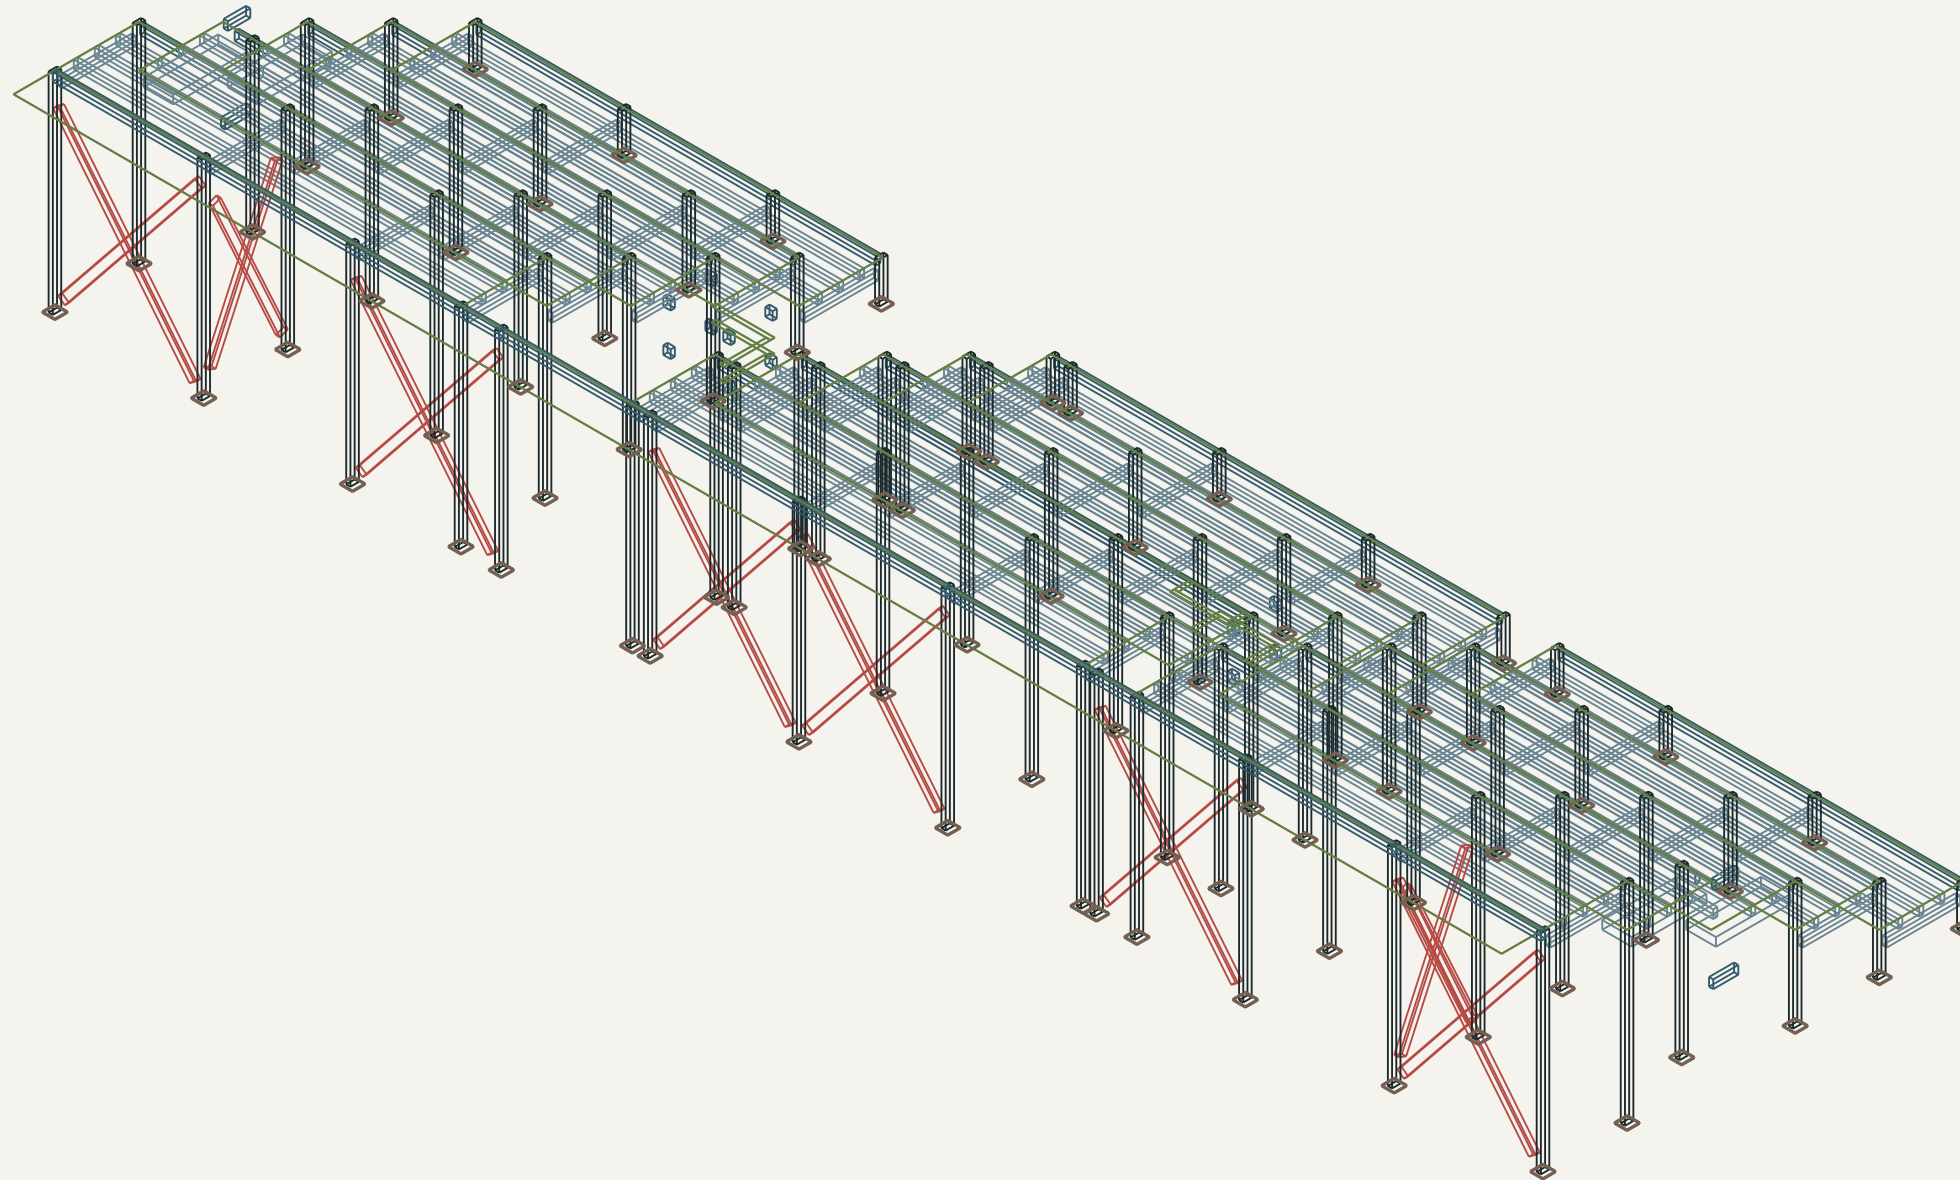

Urutan: survei beton / marking > karet & dudukan > kolom > balok & X > dek > tangga & railing.

Gunakan penyangga sementara; lepas setelah stabilitas dan semua sambungan diperiksa.