


T-01 DENAH MODUL TANGGA / TUMPUAN

09.09.2026

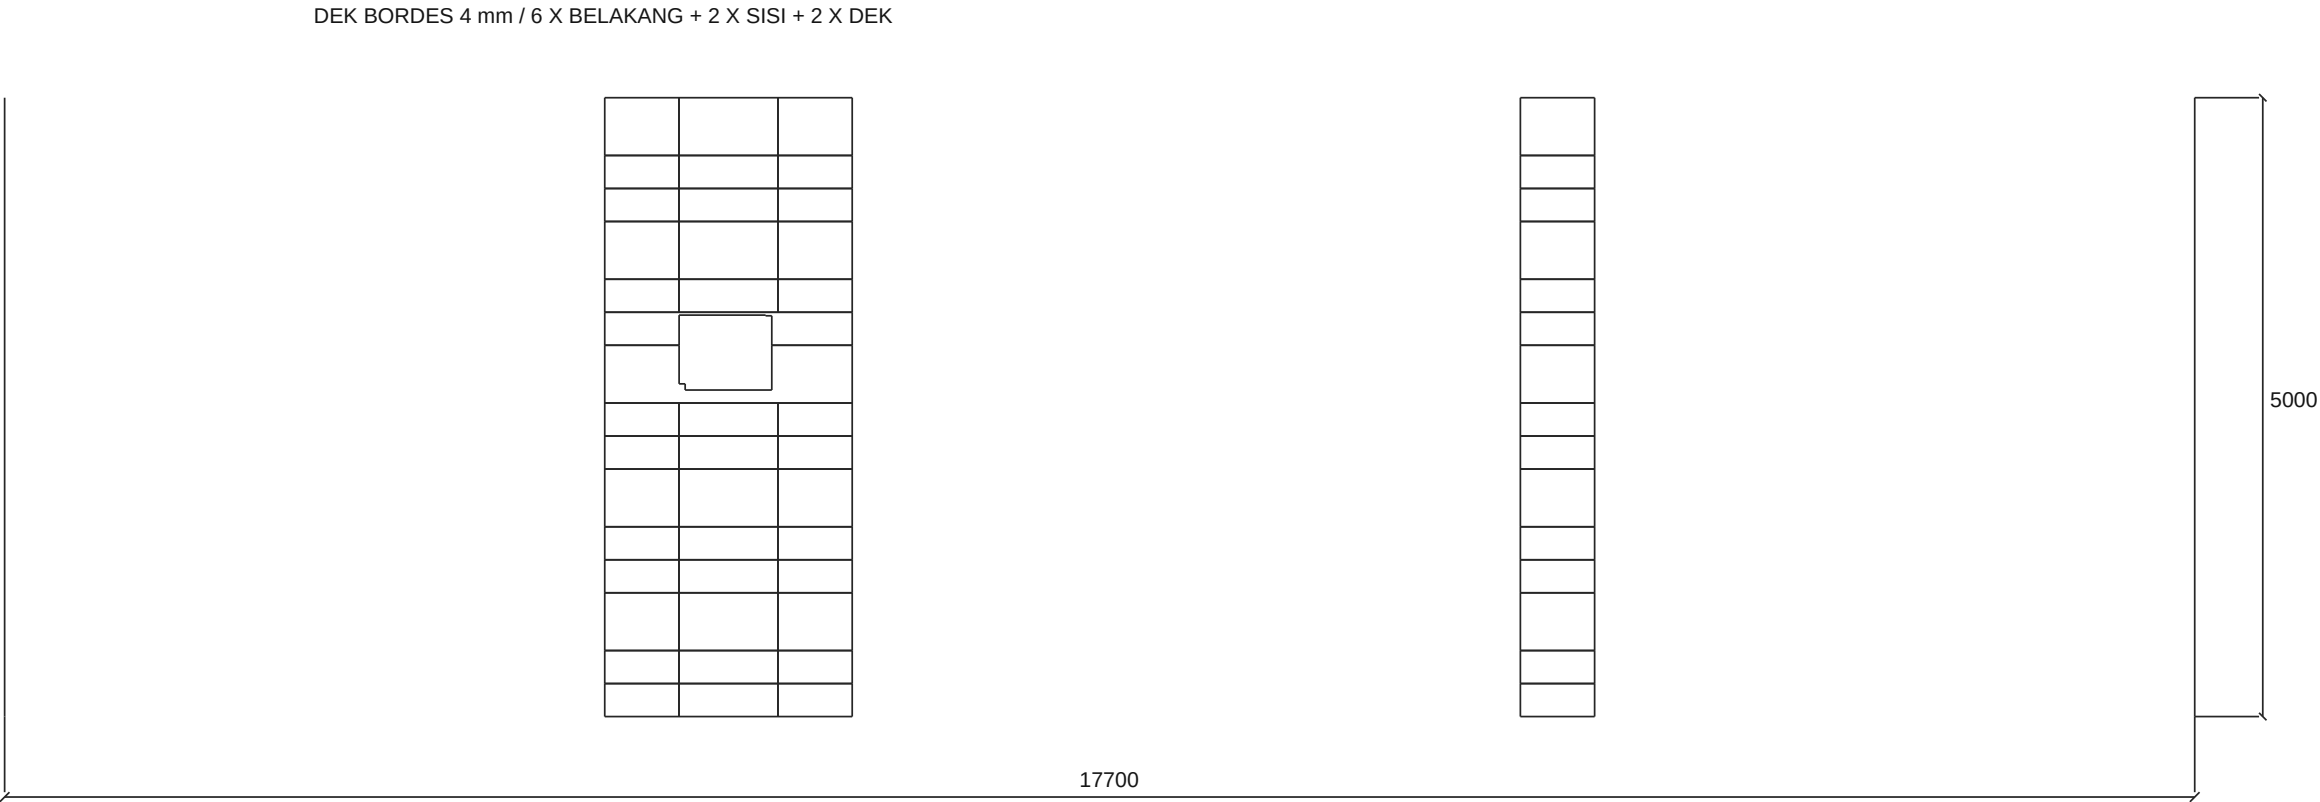

56 bidang sesuai outline IFC; luas setiap bidang cocok dengan audit Revit sebelum penggantian.


Tapak 600 / 800 / 2000; pengaku SHS40x40x2, jarak bersih <=75; stringer RHS50x100x2,3.

Stringer pada sisi dan antara: bentang pengaku <=800. Jalur ke rangka utama perlu koordinasi node.

T-02 PELAT TEKUK 3 MM / PENGAKU TAPAK


09.09.2026

POTONGAN TAPAK / t3 / SHS40x40x2

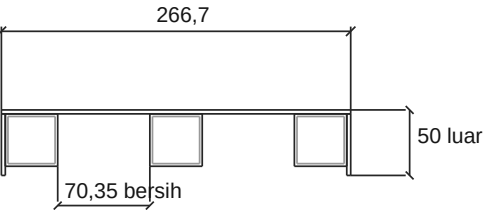

Landing466,6:5pengaku
Lebar2000:4garis stringer

DENAH / 3 PENGAKU + 2 STRINGER MODUL

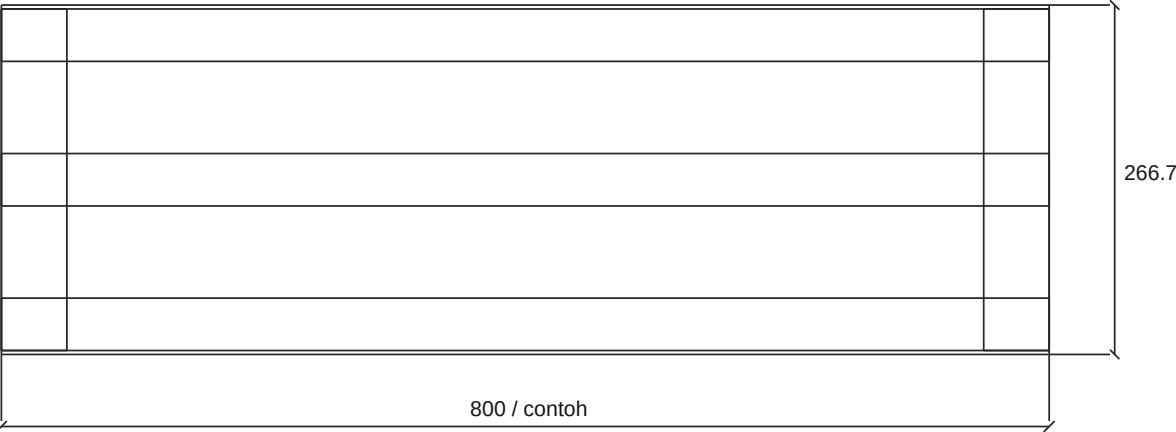


Ukuran contoh tapak 800x266,7. Lebar lain600/2000; landing dalam466,6, lihat jadwal JSON.


Dua tekukan90 derajat; dimensi luar flange50. Ri3 dan K0,40 adalah asumsi uji kupon bengkel.

Celah bersih penyangga <=75; antiselip agregat di seluruh bidang injak, nosing warna kontras.

RHS / ujung pada x20; baut pada x45

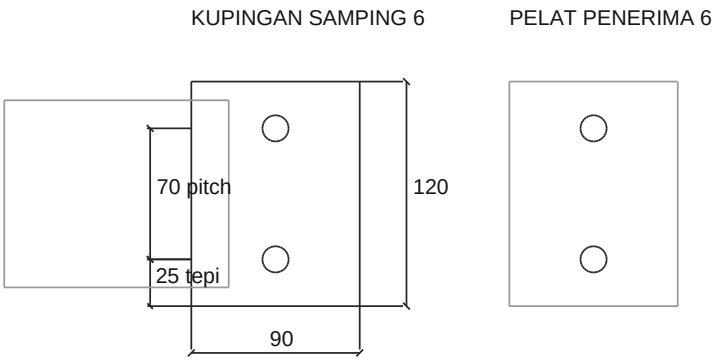

2 x M12 - lubang14 / baut40 nominal

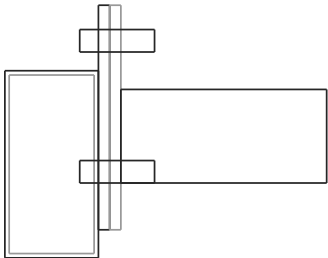

SKEMA PASANG / pelat sambungan di luar profil

Akses kunci >=30; detail penerima mengikuti node rangka

Dudukan gravitasi dan pengaku stabilitas diperiksa terpisah

Usulan kupingan samping6mm 90x120:2bautM12 kelas8.8, lubang14, 2ring/baut; bukan end plate menutup RHS.


Las sudut kaki3mm di bengkel; panjang efektif dan pelat penerima harus dihitung dari gaya node.

Baut mengikat kupingan di luar rongga RHS; jangan kencangkan langsung menekan dinding hollow2,3mm.

T-04 BENTANGAN / NESTING / URUTAN KERJA

09.09.2026

56 BLANK / 8 LEMBAR / LUAS 16.484 m2

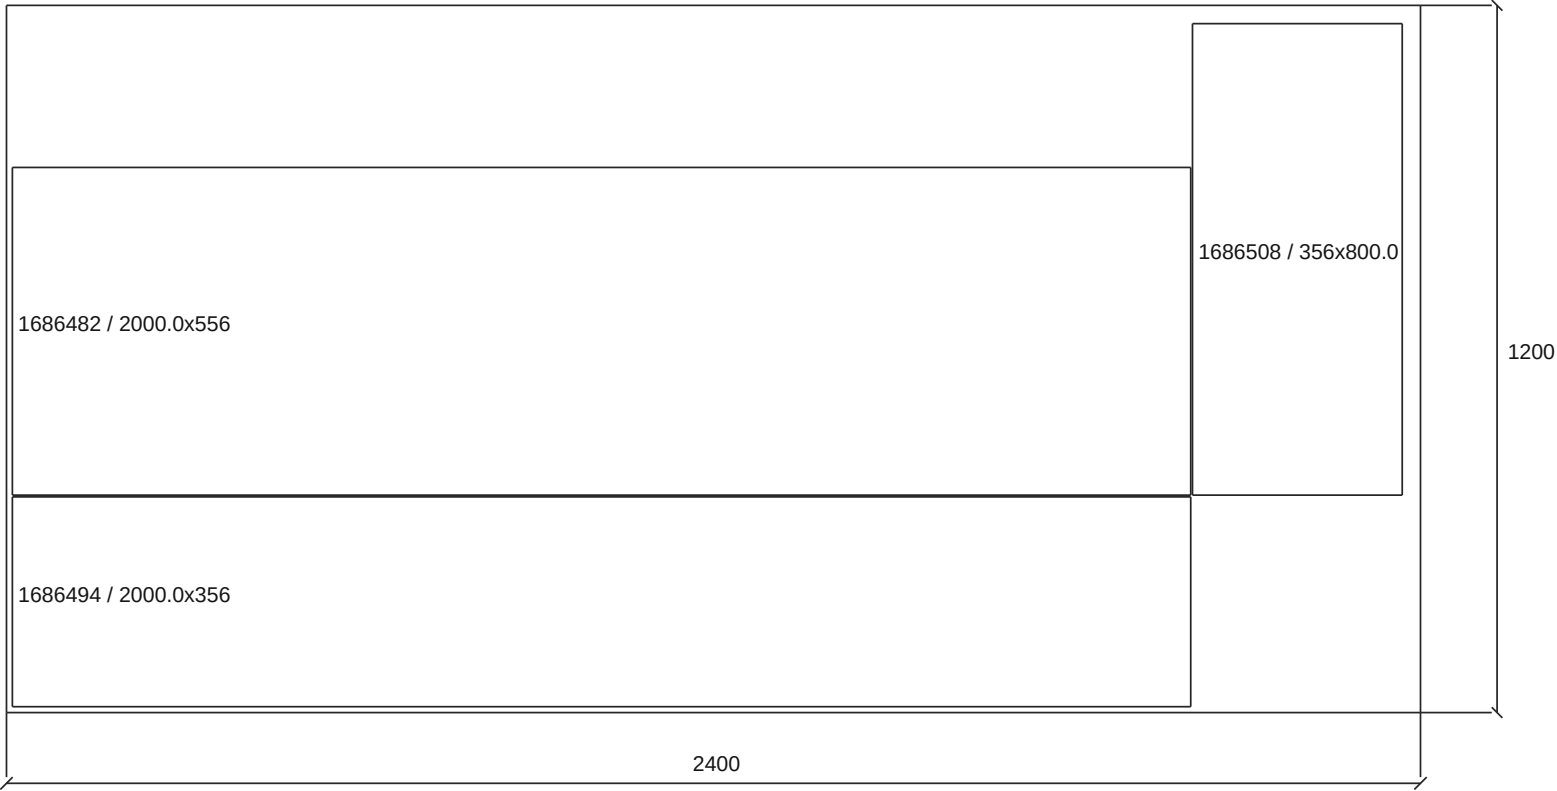

Contoh flat tapak266,7: 356 mm; landing466,6: 556 mm

BD = 5.403 mm per tekukan (asumsi)

Stok1200x2400, trim10mm, kerf3mm. Pilihan terbaik dari160varian potong lurus; bukan optimum global.


BD pertekuk = $2(R_i+t) - \pi/2(R_i+K.t)$; blank = $D+2x50-2BD$, dibulatkan ke atas1mm.

Ukur > kupon tekuk > potong dan bor > tekuk > las jig > trial fit > cat > baut lokasi > touch-up.

mm / NTS | LOD200 koordinasi; detail usulan terukur, belum rilis fabrikasi.

T-05 PENUTUP 2 MM / TAMPAK DAN TAKIKAN

09.09.2026

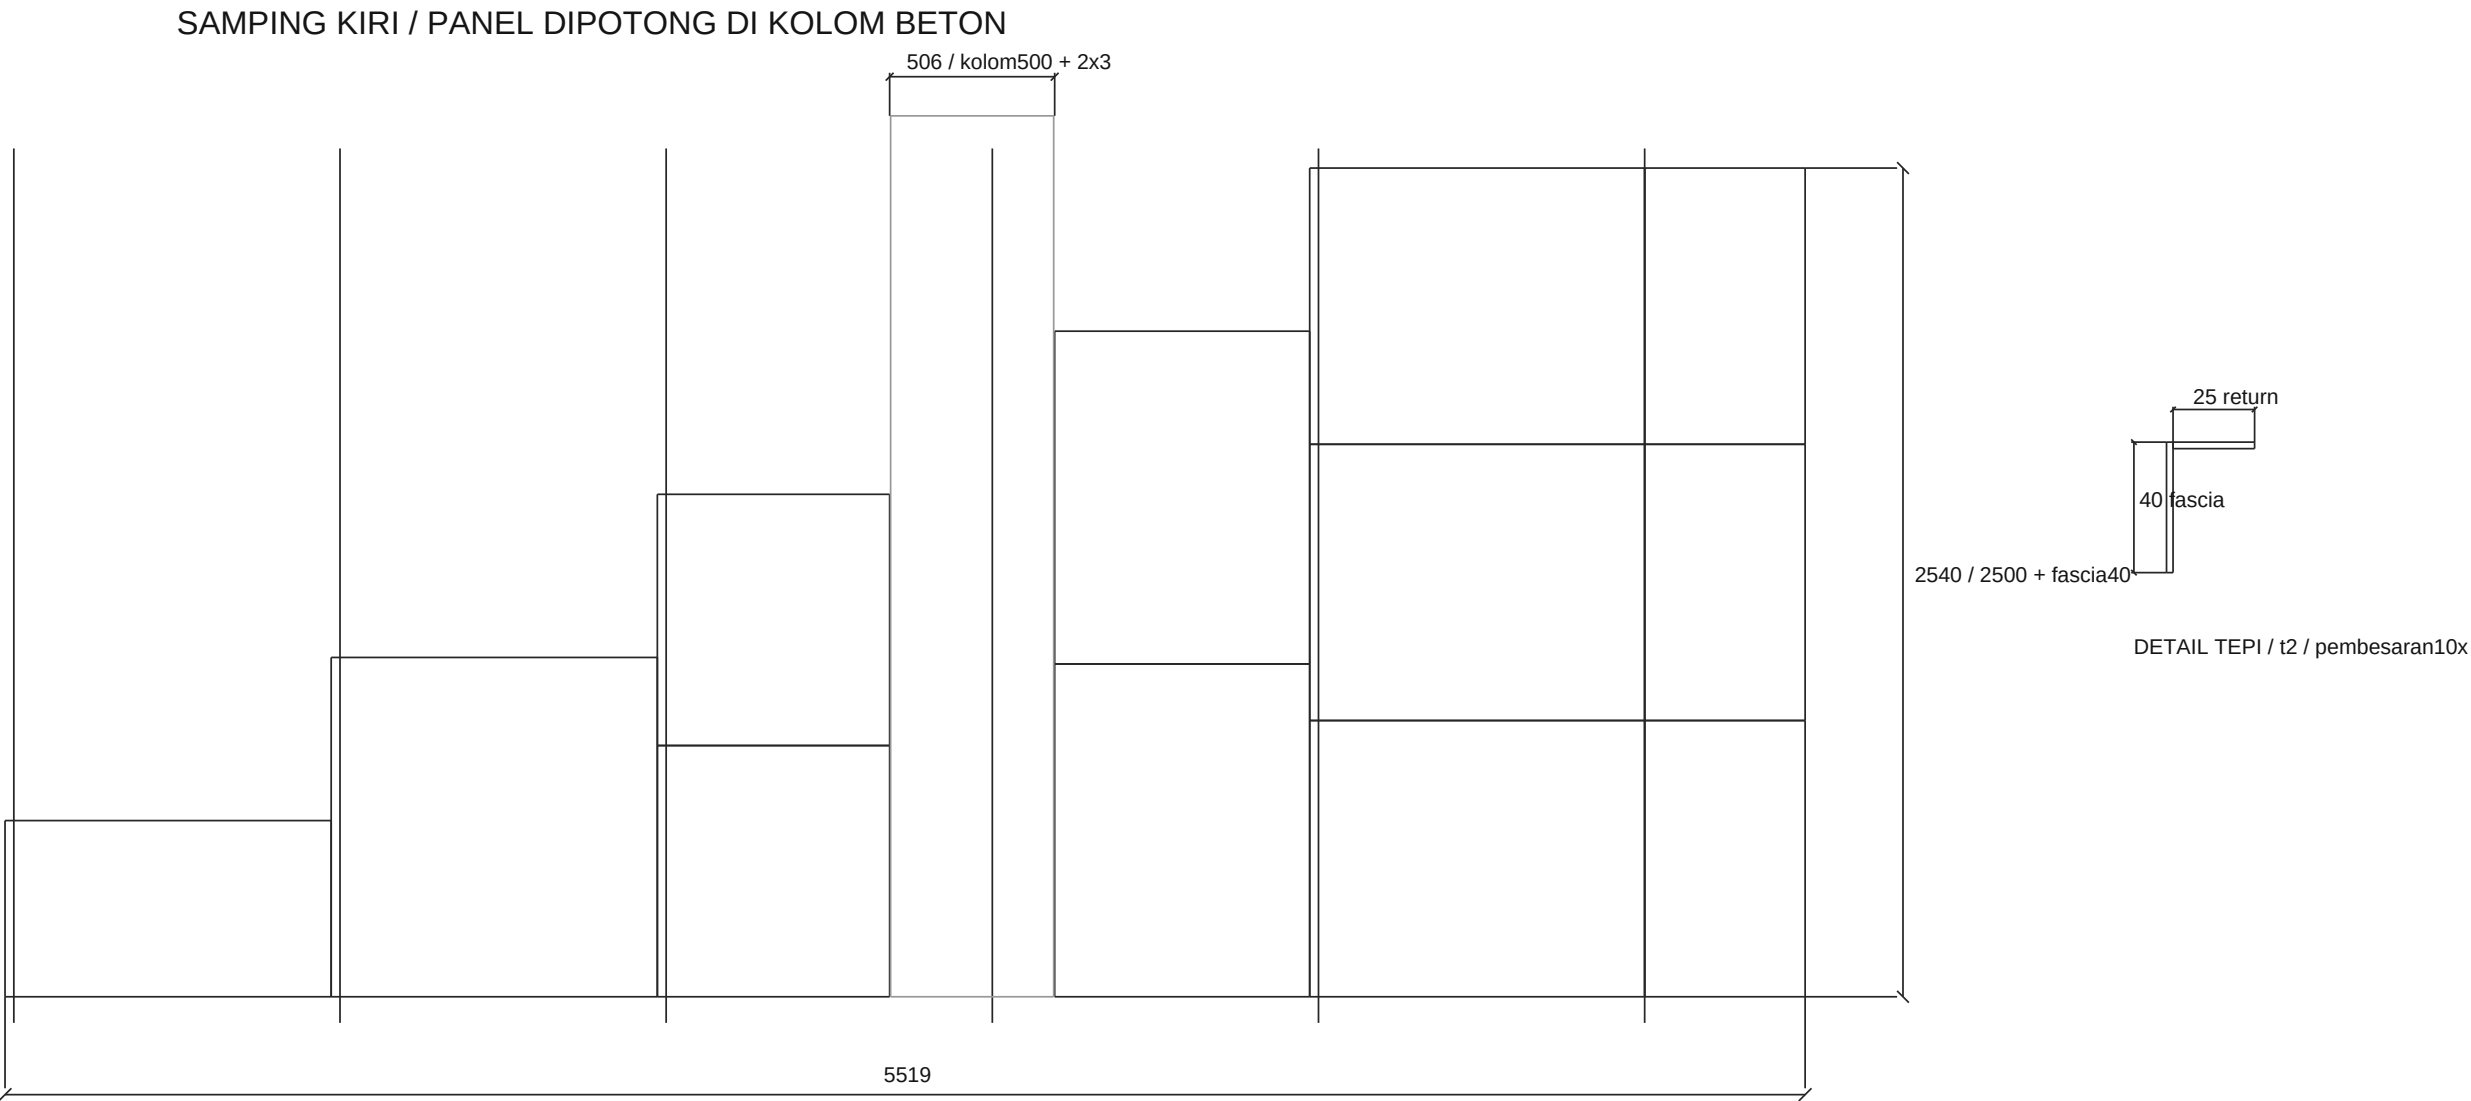

Riser, fascia dan sisi tertutup; belakang dan bawah terbuka. Semua permukaan baja dicat.



Penutup di luar muka balok. Return25mm; empat kolom beton diberi celah3mm; tidak ditutup menembus beton.

310 bagian native / 62.978m2 / 988.750kg teoritis. Sekrup dan backing mengikuti detail pemasangan.

T-06 BRACING X / POSISI REVISI NATIVE

09.09.2026

TAMPAK BELAKANG / NODE +150 DAN +2350

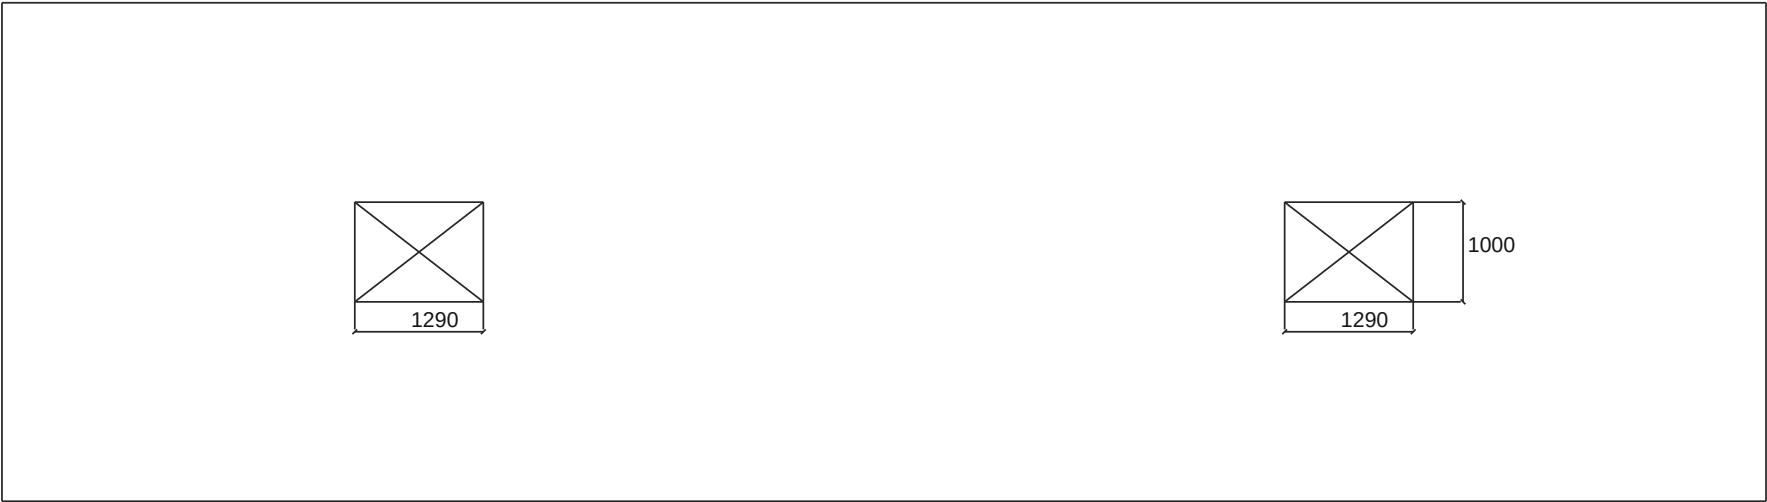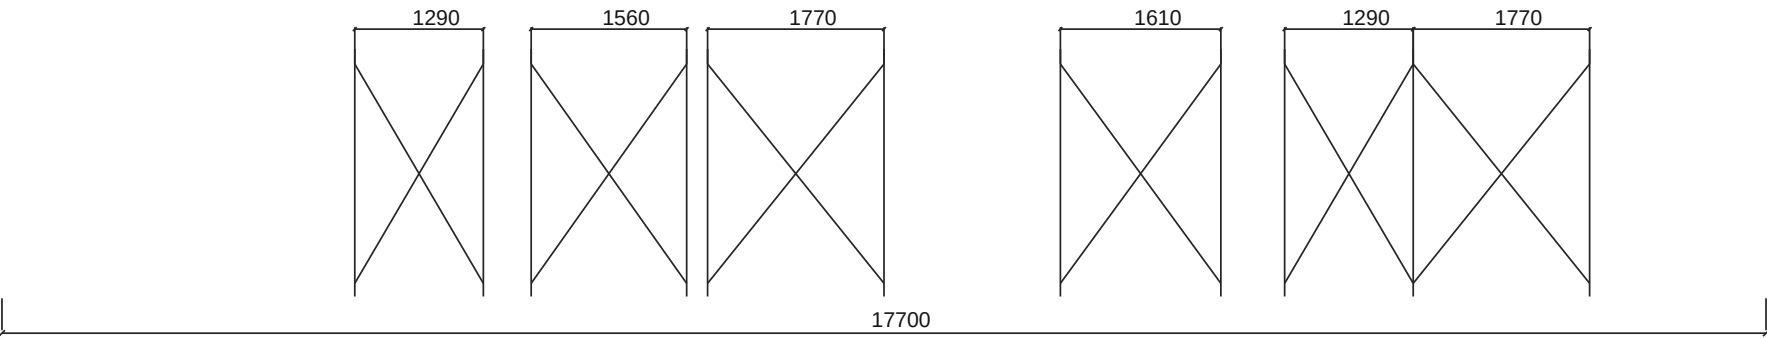

DENAH X MENDATAR / DI BAWAH DEK +1500

10setX:6belakang,2sisi tetap,2mendatar di bawah dek+1500.12diagonal belakang lama telah dihapus.
X belakang memakai bidangY4970/5030 agar diagonal bersilang tanpa bertabrakan. Sambungan ujung belum final.
X mendatar: lapis atas1325..1375 dan bawah1265..1315; celah10mm. Ukuran profil RHS50x100x2,3.